



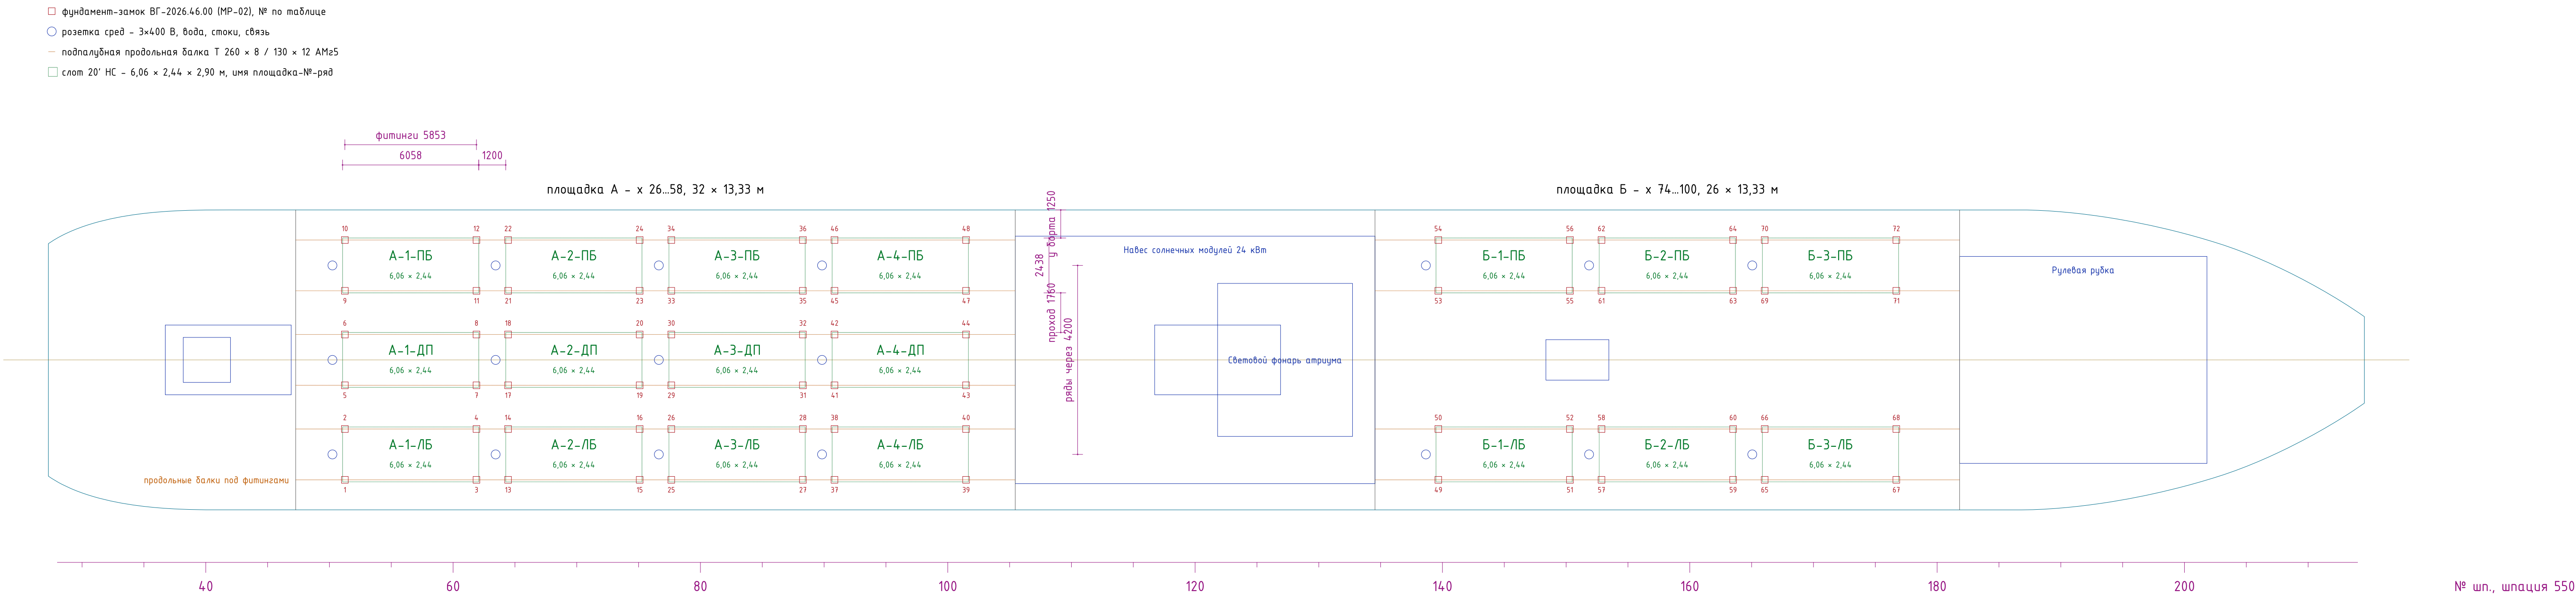


Разрез по оси опоры и по болтам, М 1 : 2

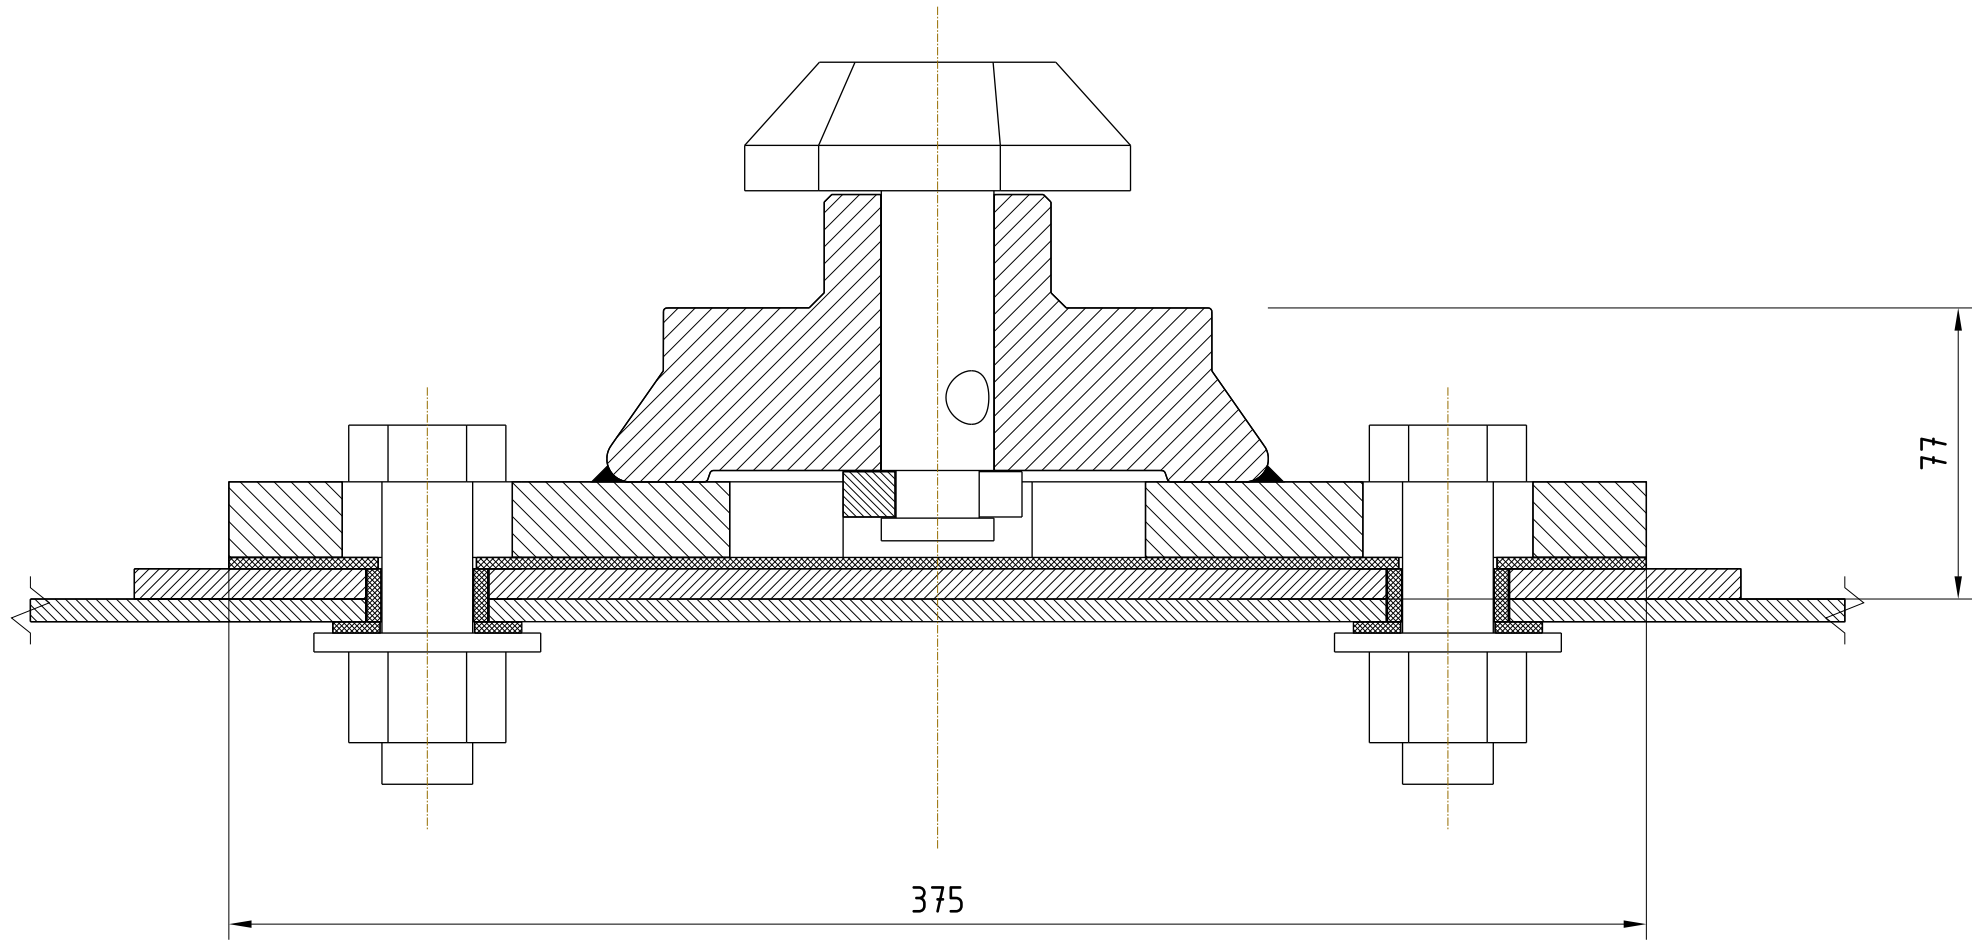

Фундамент-замок	Значение
Узел	ВГ-2026.46.00, КД - СБ, детали, литейная оснастка
SWL опоры – отрыв, сжатие, сдвиг	10, 100, 55 кН
Высота опоры над настилом	77 мм
Масса опоры с листом, всех 72	30,1 кг, 2,16 т
Поворот рукоятки	74° от выреза до выреза
Балка под линей фитингов	Т 260 × 8 / 130 × 12 АМз5, пролёт 2,2 м

Опоры под модулем 20’ НС, М 1 : 20 (контур модуля – тонкой штрихпунктирной)

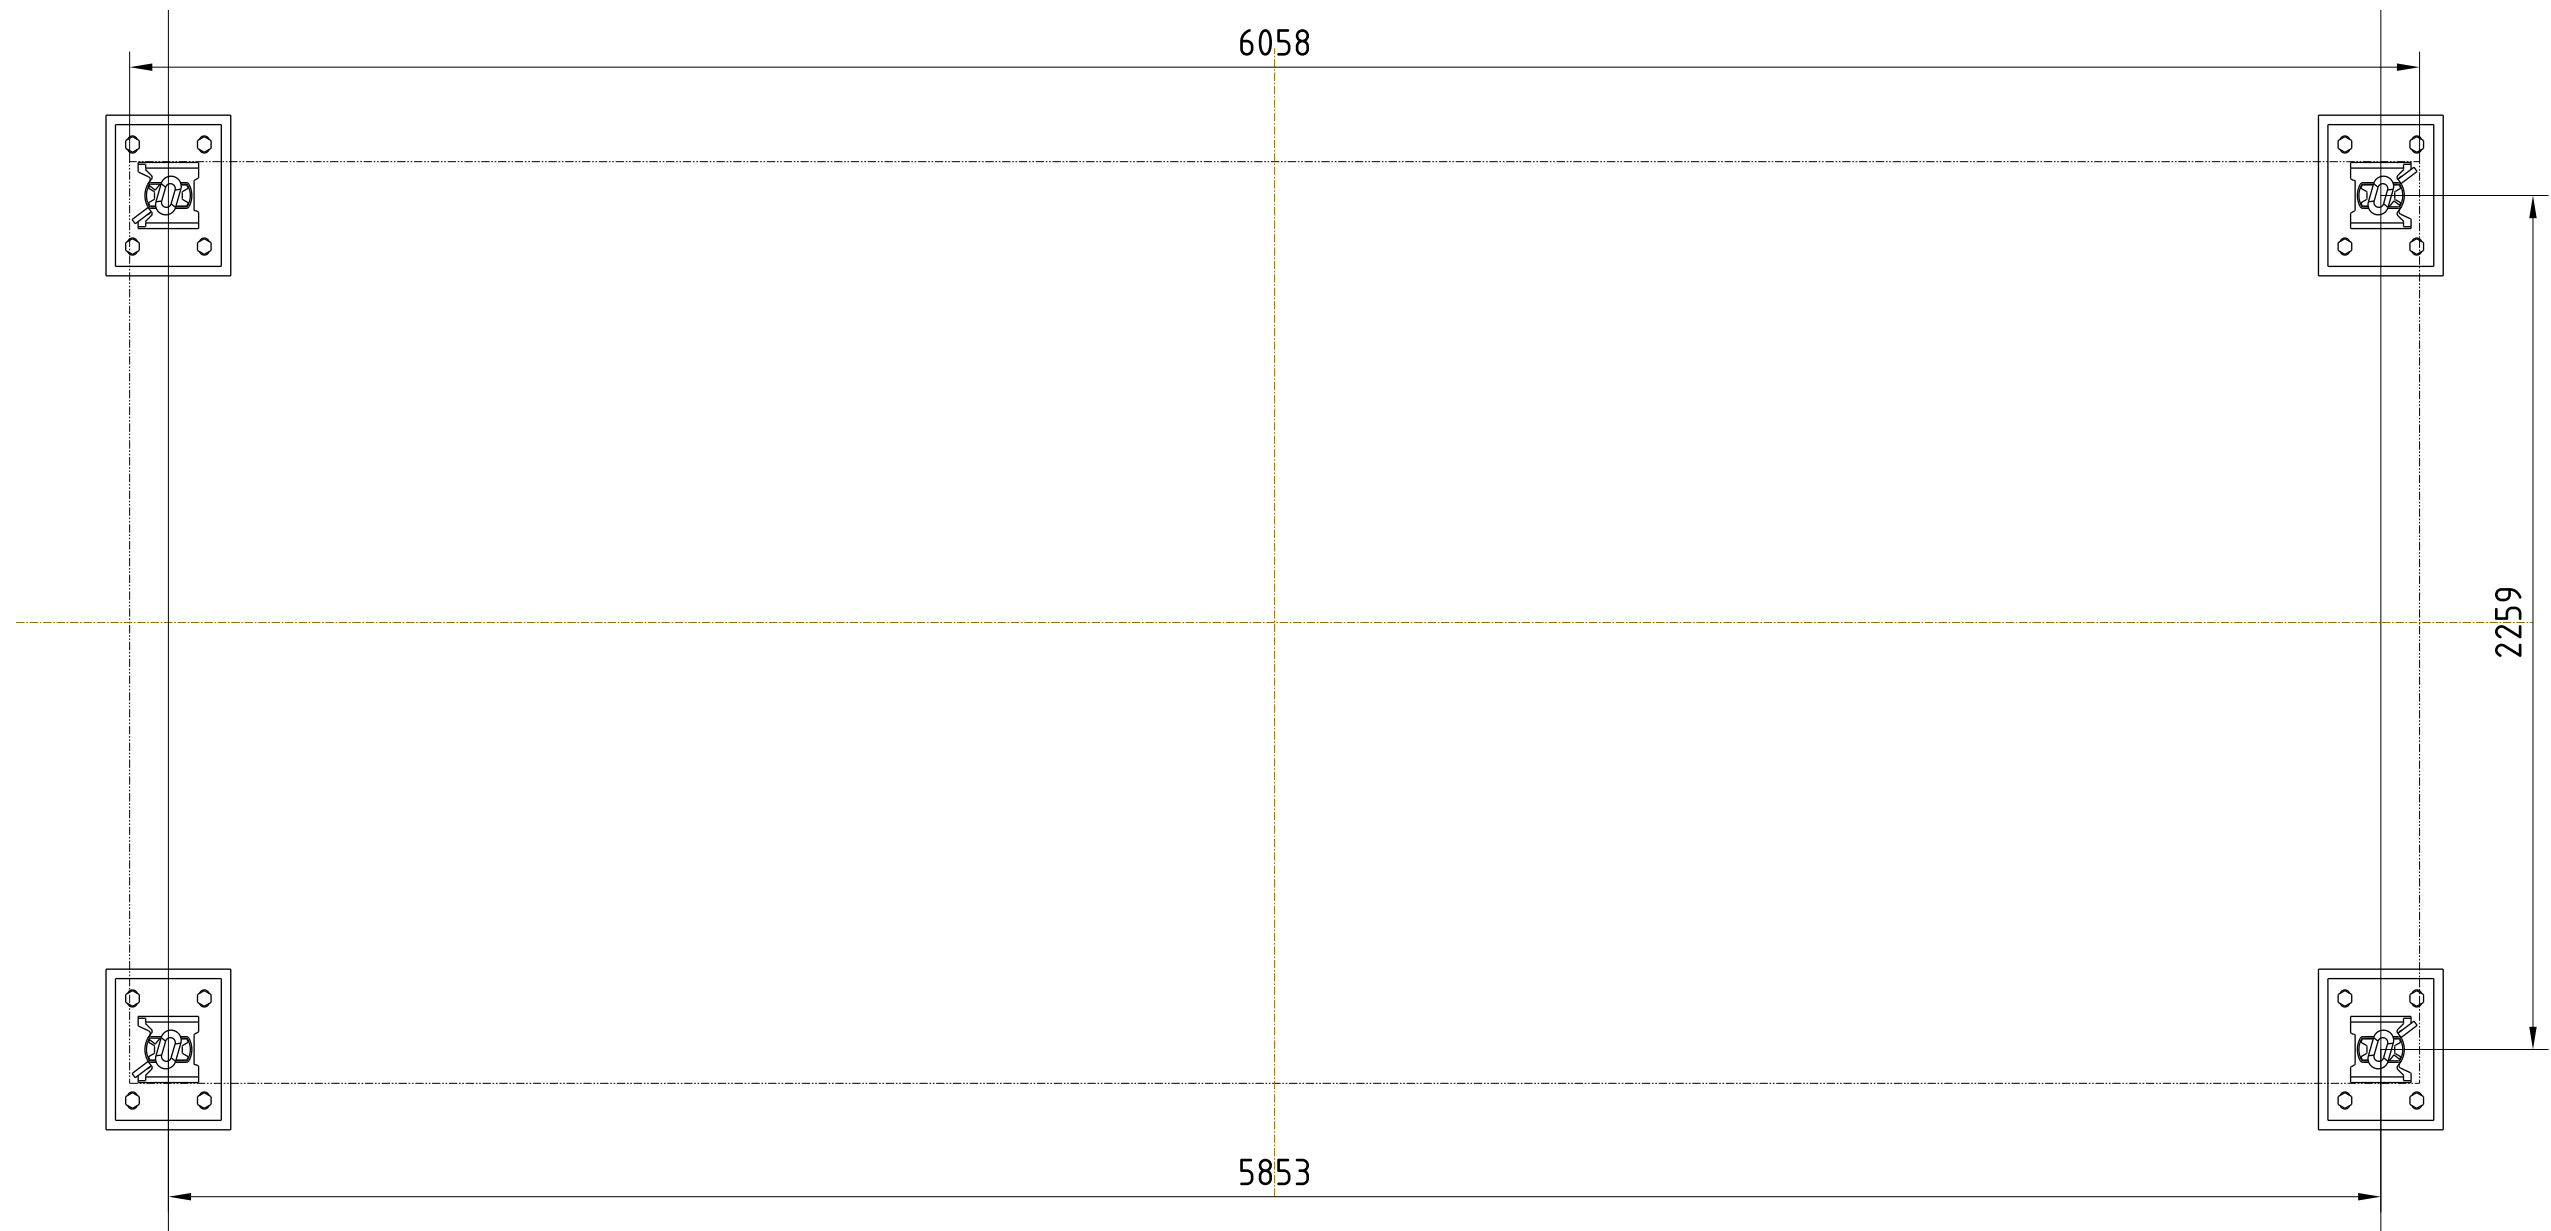


рукоятки смотрят в торцевые проходы 1,2 м, оси опор – на линиях подпалубных балок


- Технические требования**
- Узел – фундамент-замок ВГ-2026.46.00, твистлок «ласточкин хвост» – литой корпус 20ГСЛ приварен к платку 09Г2С, запор 40Х. КД, расчёт по качке судна и технология – в документации узла.
 - Опора ставится над подпалубной балкой на лист АМз5, приваренный к настилу. Болты М24 А4–80 в изолирующих втулках, прокладка – стеклотекстолит.
 - Корпуса кормовых опор слота – рукояткой в корму, носовых – в нос, рукоятка выходит в торцевой проход, где стоит человек при смене темы.
 - Модуль садится на плечи корпусов, центраторы входят в отверстия фитингов. Поворот рукоятки на 74° от выреза до выреза разворачивает голову запора поперёк отверстия фитинга.
 - Модули тяжелее 10 т (бассейн) ставятся только в ряд ДП.
 - Размеры в миллиметрах, разрез – М 1 : 2, раскладка опор – М 1 : 20.
- УЖЦ ОСК 2026 · «Волжский Горизонт» · ПБ «Без границ»

Фундамент-замок под модуль	
Установка на солнечной палубе, 72 шт. на судно	
ВГ-2026 МР-02	Масштаб 1 : 2
20ГСЛ, 09Г2С, 40Х, АМз5	Формат А1


1. Тема «базовая» – солярий и прогулочная палуба, модулей нет

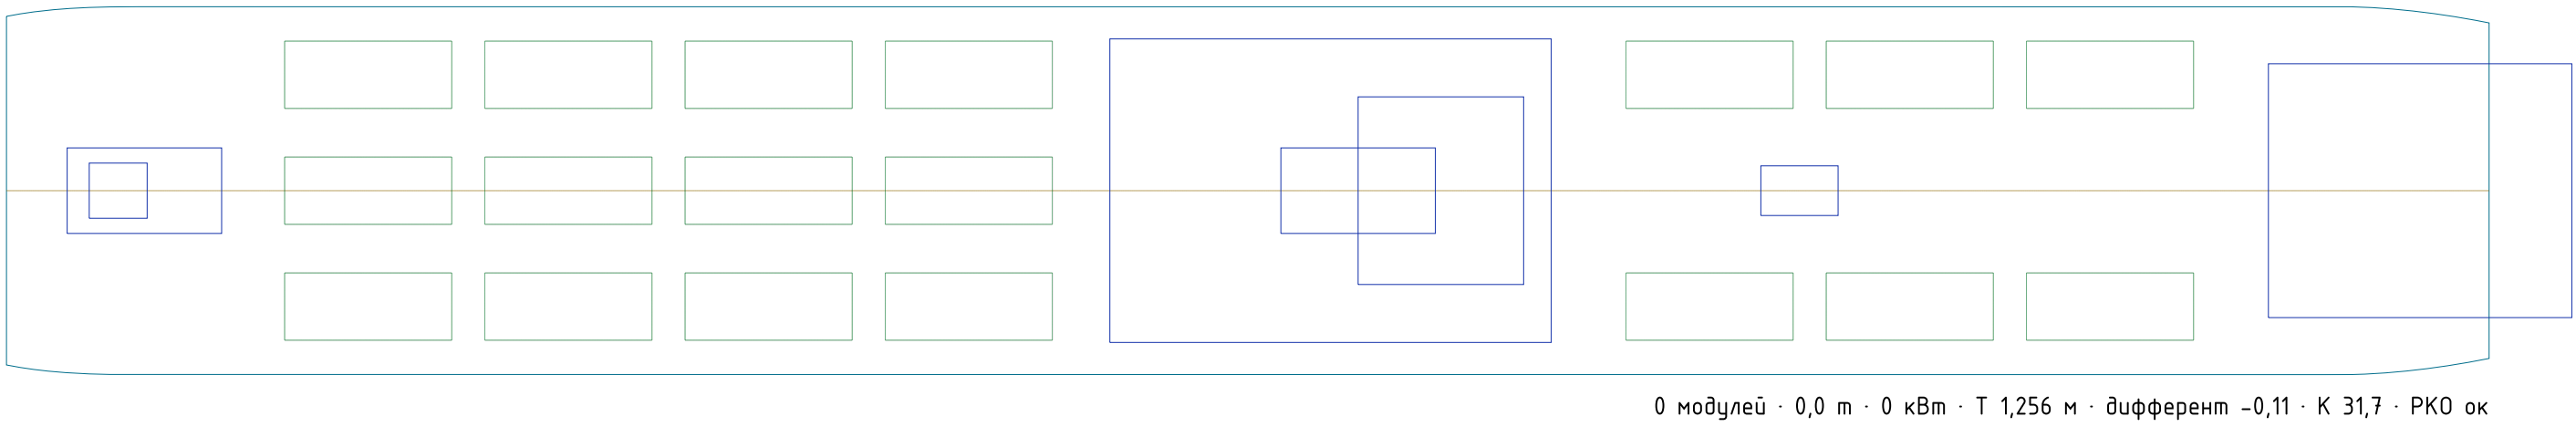


2. Тема «деловая» – деловые круизы – восемь кабинетов и переговорных по бортам, бар

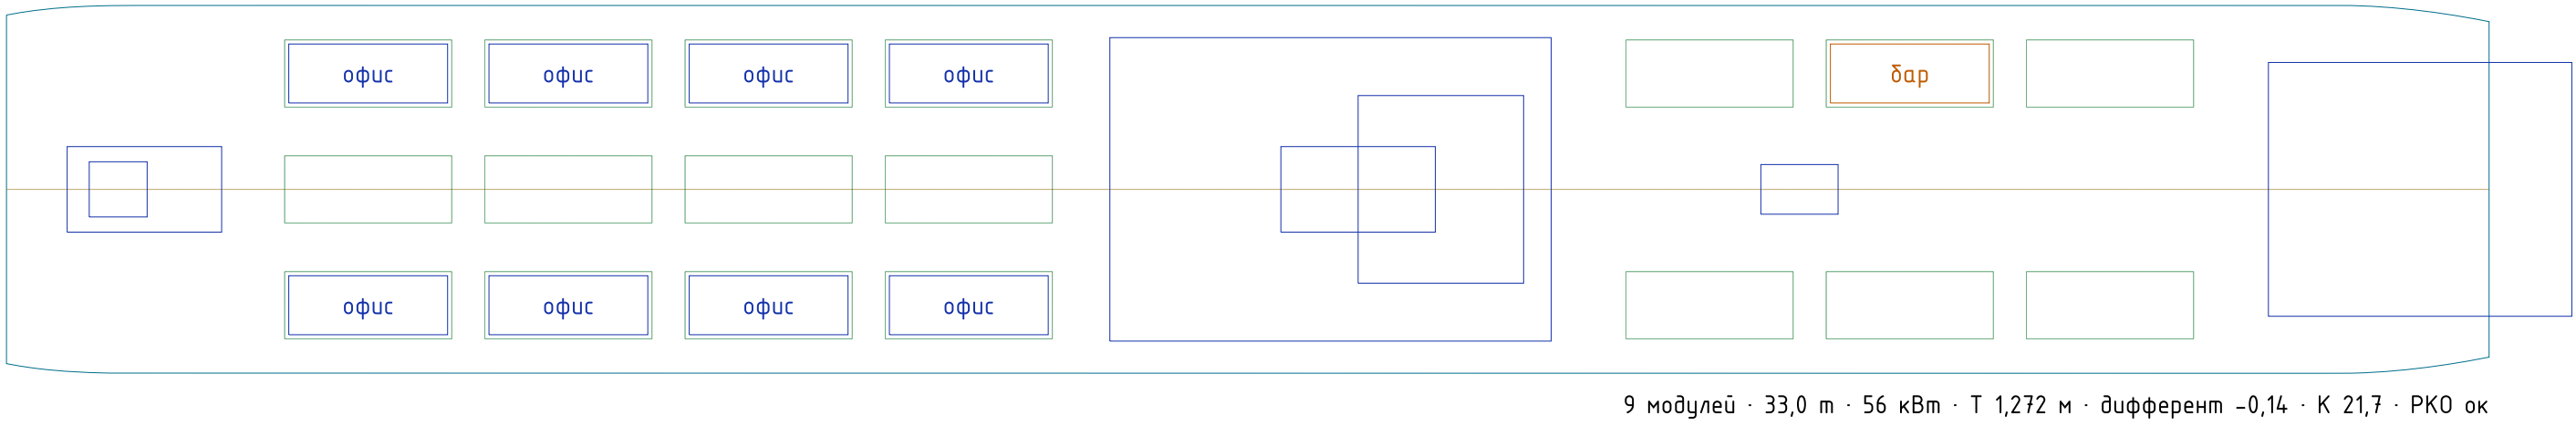


3. Тема «оздоровительная» – термы на палубе – четыре сауны с купелями, два мелких бассейна в ДП, два кабинета процедур, бар

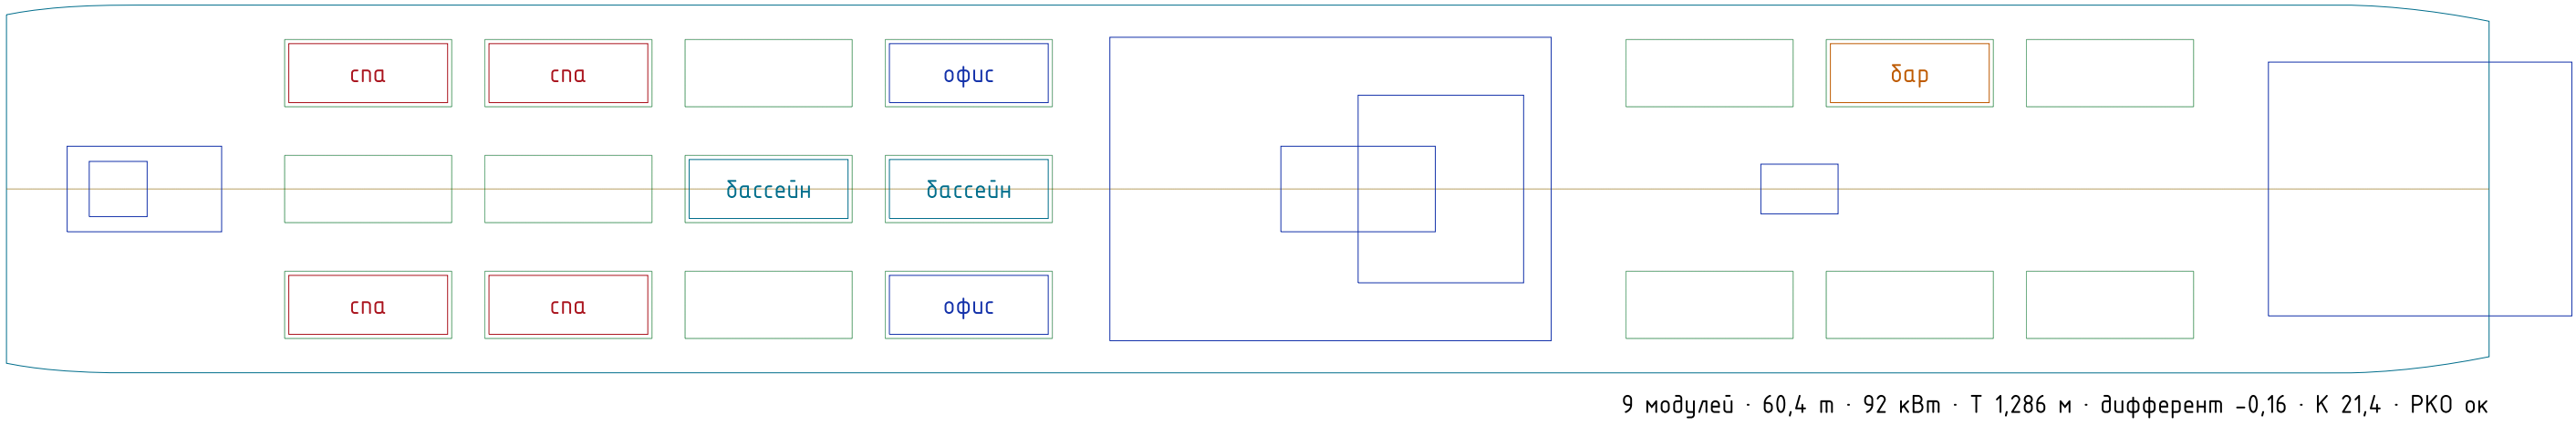


4. Тема «детская» – детские круизы – шесть игровых модулей, клубный блок для анимации, бар

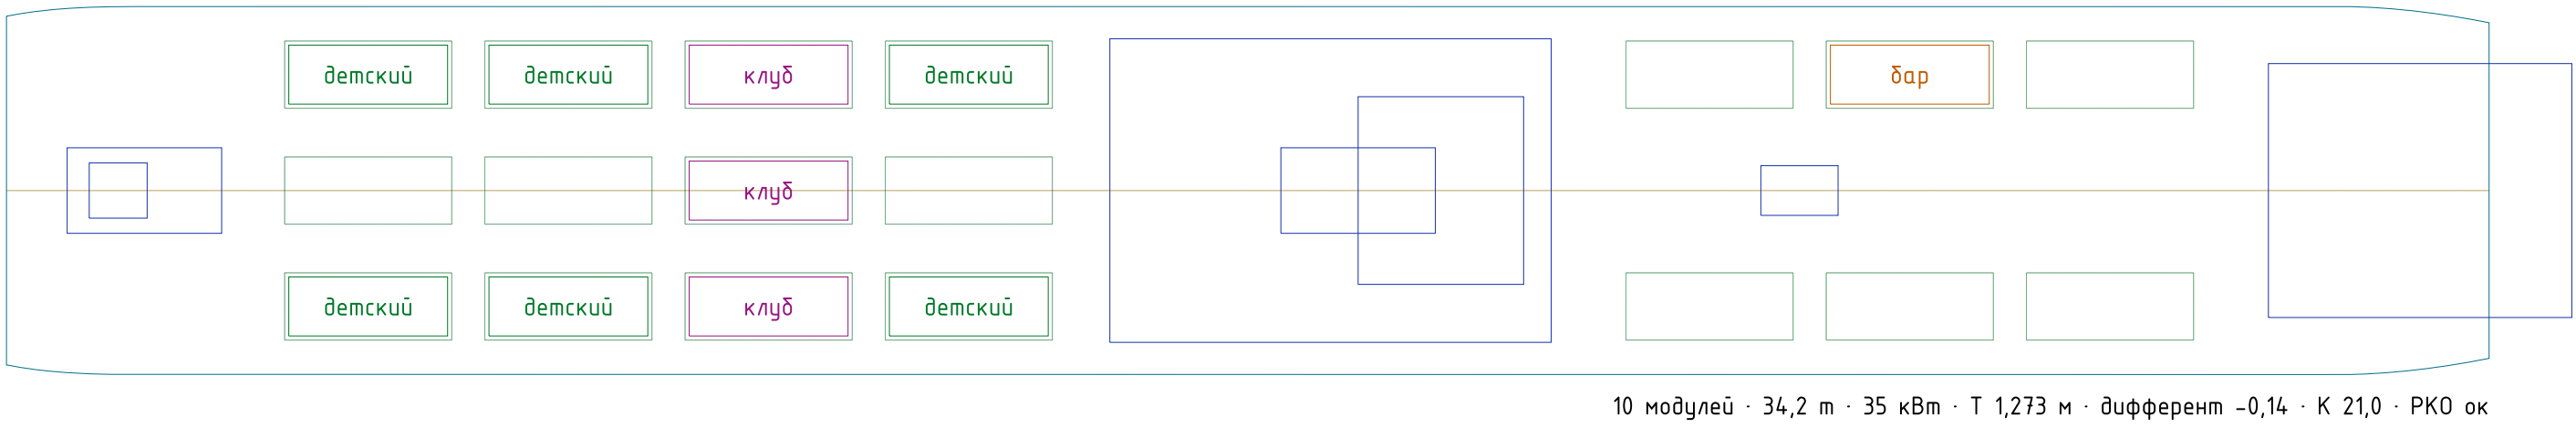

5. Тема «событийная» – диско, кино, театр, свадьбы – два клубных блока по три секции, гримёрная, бар

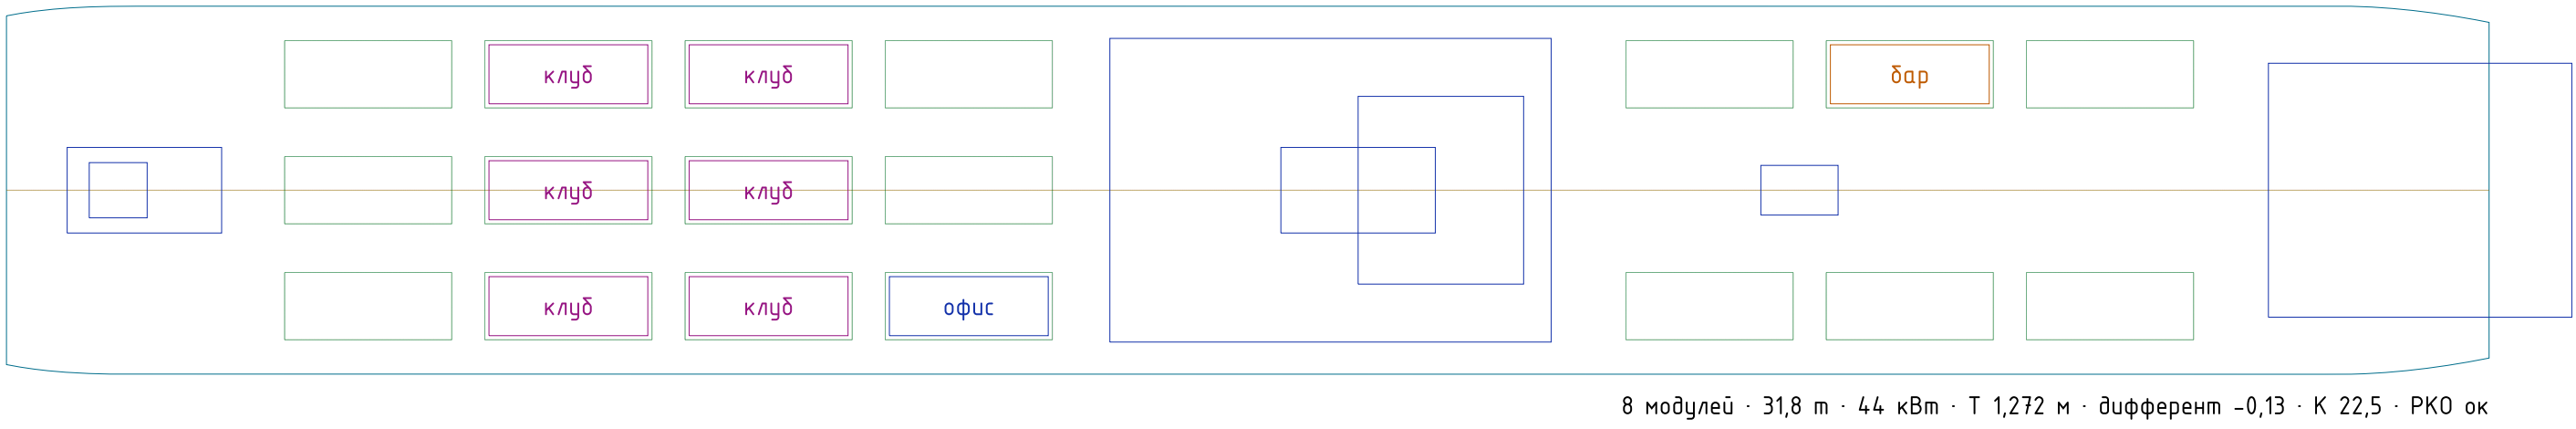

6. Тема «президентская» – остров на плаву – люкс из двух секций с террасой, сауна, мелкий бассейн, кабинет, бар

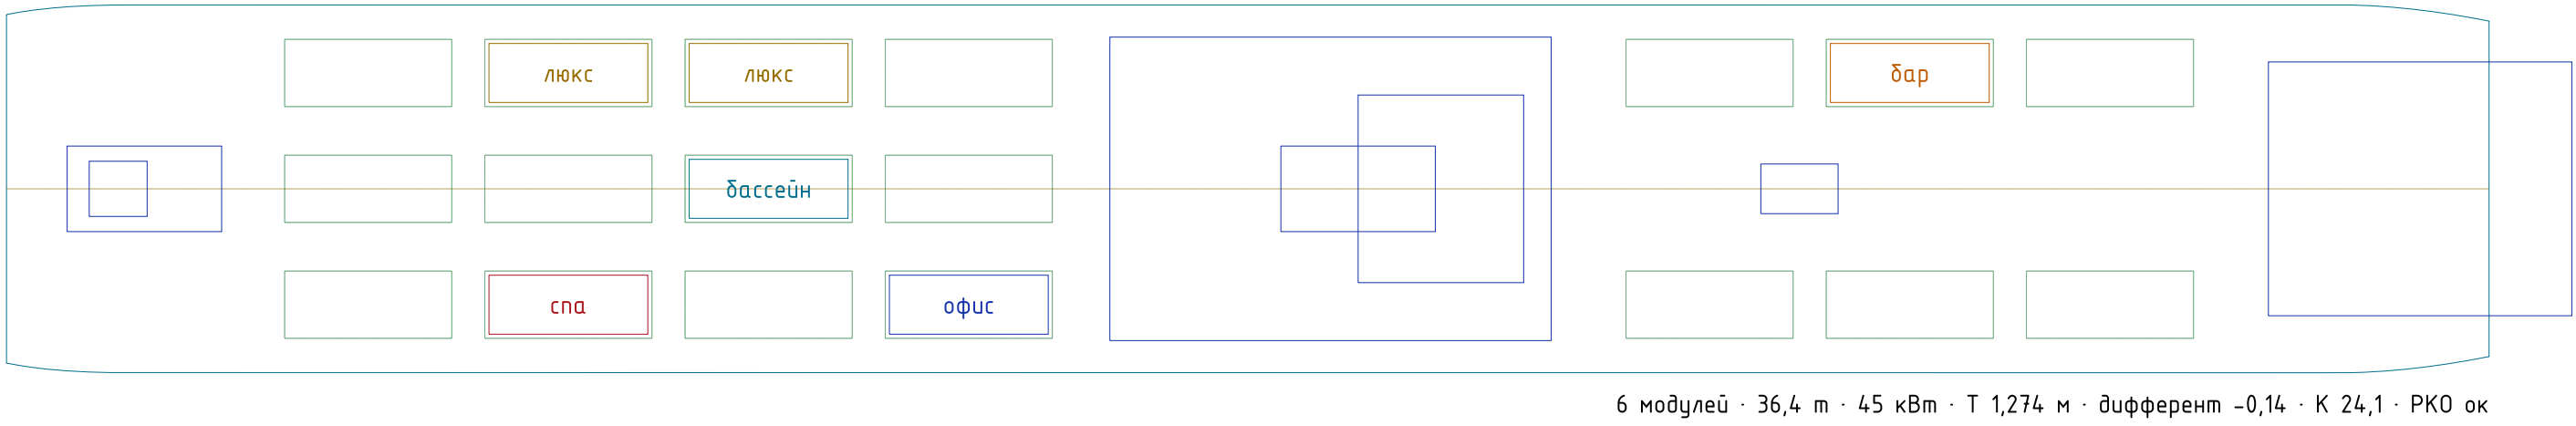

Тема	Мод.	Масса, т	кВт	Т, м	Дифф., м	К	h, м	Вода / стоки	Годна
базовая	0	0,0	0	1,256	–0,11	31,7	15,5	0 / 0	да
деловая	9	33,0	56	1,272	–0,14	21,7	15,2	1 / 1	да
оздоровительная	9	60,4	92	1,286	–0,16	21,4	14,9	7 / 7	да
детская	10	34,2	35	1,273	–0,14	21,0	15,2	1 / 1	да
событийная	8	31,8	44	1,272	–0,13	22,5	15,2	1 / 1	да
президентская	6	36,4	45	1,274	–0,14	24,1	15,2	5 / 5	да

Модуль	Масса, т	кВт	А	Вода	Что это (принято по рынку, уточняется по спецификации поставщика)
офис	3,6	6	32	–	переговорная или кабинет на 6..8 мест, панорамные окна, сплит-система, связь
спа	5,5	15	63	да	сауна с электрокаменкой 12 кВт, купель 1 м³, душ, дерево, своя вентиляция
бассейн	13,5	6	63	да	чаша 5,5 × 2,2 м глубиной 0,8 м (9,7 м³ воды), насос, фильтр и подогрев, борти
детский	3,0	2	32	–	игровой модуль с откидным бортом-верандой, мягкое покрытие, сетка-ограждение
клуб	4,0	5	32	–	секция зала. Три секции в одном ряду поперёк палубы под общим тентом – диско,
люкс	4,8	5	32	да	секция президентского люкса – спальня или гостиная с санузлом, две секции и те
бар	4,2	8	63	да	бар-кухня на палубе – мойка, холодильники, кофемашина

офис спа бассейн детский клуб люкс бар

Технические требования

- Слоты – по МР-01, фундаменты – по МР-02. Тема меняется сменой модулей на тех же фундаментах (концепция «трансформер»).
- Предел массы на палубе 85 т (задание) при 89 т до расчётной осадки 1,30 м. Посадка и остойчивость каждой темы проверены по нормам РКО.
- Мощность модулей – из резерва электростанции на стоянке 502 кВт. На мелководье резерв 30 кВт, печи саун и подогрев бассейна – от батарей 600 кВт·ч или отключаются.
- Бассейн – самый тяжёлый модуль (13,5 т с водой), глубокий бассейн 18,0 т в темы не включён.
- Массы и мощности модулей приняты по контейнерным модулям рынка и заменяются на данные поставщиков без изменения листа.

УЖЦ ОСК 2026 · «Волжский Горизонт» · ПБ «Без границ»

Темы круизов – раскладки модулей по слотам

Модульное решение «трансформер» · 6 тем · площадки А и Б	
ВГ–2026 МР–03	Масштаб 1 : 250
Контейнеры 20' НС ISO 668	Формат А1