

№	Помещение	Площадь, м ²	Шпангоуты	х, м
1	Кормовая терраса, транцевая аппарель - аппарель 9,0 x 3,6 м	70	0..9	0.0..5.0
2	Гараж на 4 автомобиля класса Б, комплекс высадки на берег - телескопический трап ЛБ, пост якорной, швартовное устройство	204	9..36	5.0..20.0
3	Кормовой трап-холл, лифт, санузлы	86	36..47	20.0..26.0
4	Блок экипажа - столовая, кают-компания, офисы, каюты экипажа по бортам	115	47..62	26.0..34.0
5	Каюты стандарт по бортам, каюты экипажа внутри - М4 у кормового лифта	345	62..105	34.0..58.0
6	Атриум - ресепшен, лобби, главный трап, два лифта, галереи к колёсам - выгородки ГЗД и редукторов по бортам, медпункт и изолятор в носовом углу ЛБ	178	105..135	58.0..74.0
7	Камбуз, хлебопекарня, посудомоечная, раздаточная - шахта выхода ГДГ по ДП	144	135..153	74.0..84.0
8	Главный ресторан - две смены	222	153..182	84.0..100.0
9	Каюты стандарт по бортам, семейные внутри	115	182..196	100.0..108.0
10	Носовой трап-холл, лифт	86	196..207	108.0..114.0
11	Театр-лаунж - кино, концерты, лекторий, вечером клуб	112	207..225	114.0..124.0
12	Носовой панорамный салон-обсерватория	26	225..236	124.0..130.0
13	Открытая носовая палуба, якорно-швартовное устройство	50	236..255	130.0..140.0


Технические требования

- Уровень палубы z = 3.00 м от основной плоскости. Кают на палубе - 32.
- Размеры в миллиметрах, ось х - от кормового перпендикуляра, шпация практическая 550 мм.
- Красные линии - водонепроницаемые переборки трюма, тонкие - границы зон.
- Коридоры 1.30 м в свету, бортовой проход главной палубы 1.00 м, двери кают 0,70 (М4 - 0,90) м.
- Коды кают - Э эконом, С стандарт, Б бизнес, Л люкс, Сем семейная, Эк экипаж, М4 - доступная.

УЖЦ ОСК 2026 · «Волжский Горизонт» · ПБ «Без границ»

Общее расположение. Главная палуба

Волжский Горизонт · L = 140.0 м · В = 16.5 м · Т = 126 м · 208 пасс.	
ВГ-2026 ОР-01 главная палуба	Масштаб 1 : 200
Корпус сталь D36, надстройка АМз5	Формат А1

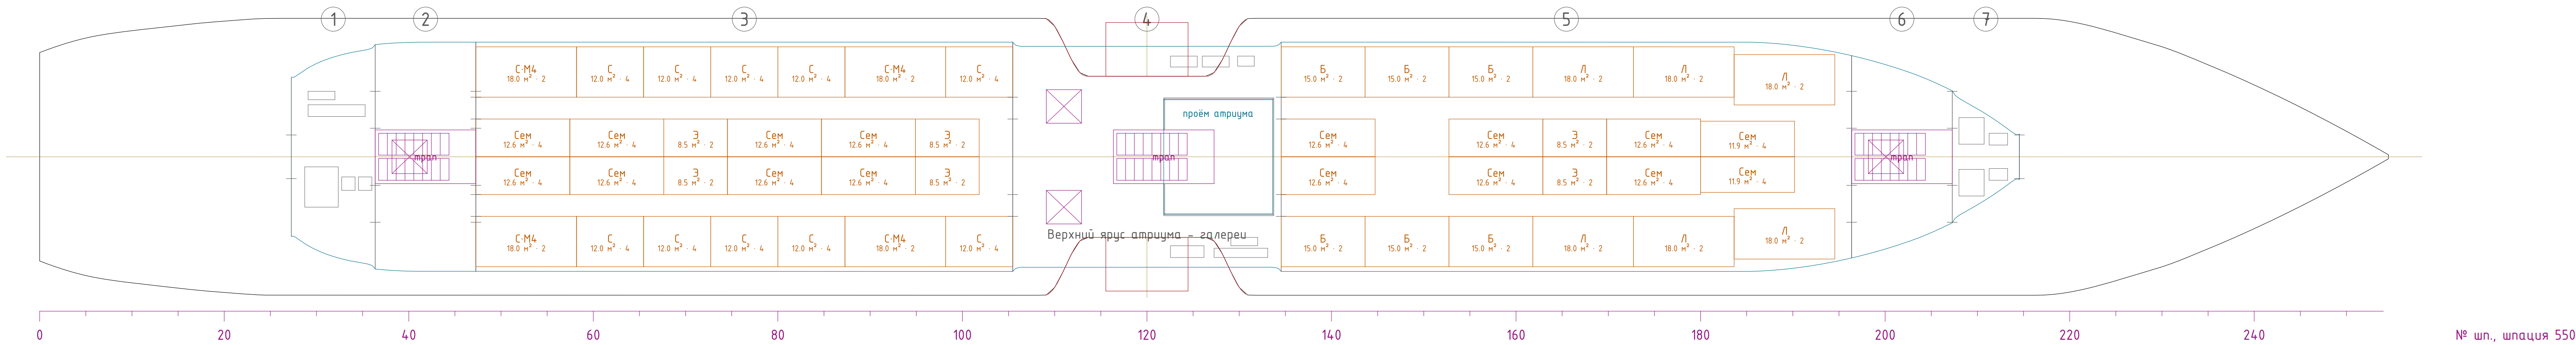

№	Помещение	Площадь, м²	Шпангоуты	х, м
1	Детский и подростковый клуб, творческая мастерская – выход на кормовую террасу–крышу	58	27..36	15.0..20.0
2	Кормовой трап-холл, лифт – аварийный ДГ 150 кВт в выгородке ЛБ	82	36..47	20.0..26.0
3	Каюты стандарт по бортам, семейные и эконом внутри	441	47..105	26.0..58.0
4	Верхний ярус атриума – галереи, бар-лаунж, фитнес ПБ – витражи в щеклах кожухов – вид на колёса	213	105..135	58.0..74.0
5	Каюты люкс и бизнес по бортам, семейные и эконом внутри	464	135..196	74.0..108.0
6	Носовой трап-холл, лифт	61	196..207	108.0..114.0
7	Спа – сауна, хаммам, процедурные	19	207..215	114.0..118.0

Технические требования

1. Уровень палубы z = 5,80 м от основной плоскости. Кают на палубе – 48.

2. Размеры в миллиметрах, ось х – от кормового перпендикуляра, шпация практическая 550 мм.

3. Красные линии – водонепроницаемые переборки трюма, тонкие – границы зон.


4. Коридоры 1,30 м в свету, бортовой проход гладной палубы 1,00 м, двери кают 0,70 (М4 – 0,90) м.

5. Коды кают – Э эконом, С стандарт, Б бизнес, Л люкс, Сем семейная, Эк экипаж, М4 – доступная.

УЖЦ ОСК 2026 · «Волжский Горизонт» · ПБ «Без границ»

Общее расположение. Средняя палуба

Волжский Горизонт · L = 140,0 м · В = 16,5 м · Т = 1,26 м · 208 пасс.	
ВГ-2026 ОР-02 средняя палуба	Масштаб 1 : 200
Корпус сталь D36, надстройка АМз5	Формат А1

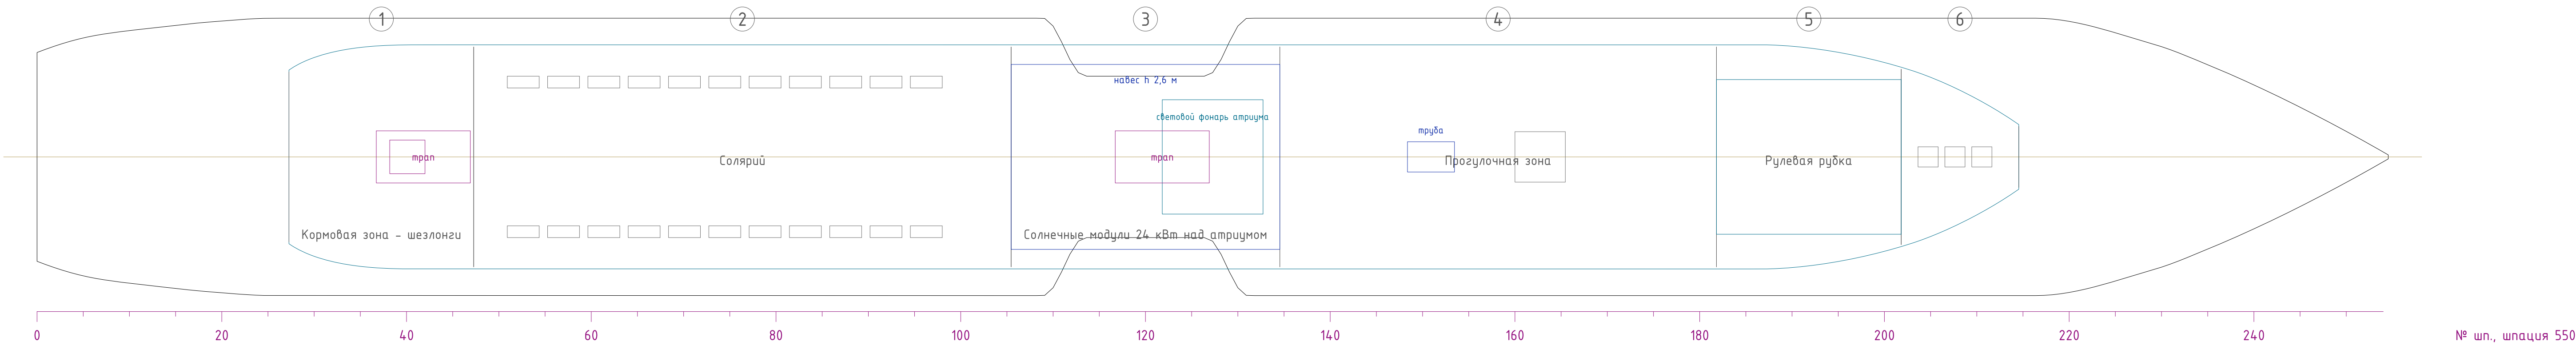


№	Помещение	Площадь, м²	Шпангоуты	Х, м
1	Кормовая зона – шезлонги, дункеровочный пост метанола ПБ	140	27...47	15.0...26.0
2	Солярий, складные тенты	422	47...105	26.0...58.0
3	Солнечные модули 24 кВт над атриумом, световой фонарь	211	105...135	58.0...74.0
4	Прогулочная зона, спортплощадка, низкая дымовая труба	343	135...182	74.0...100.0
5	Рулевая рубка – стационарная, опускной механизм убран 22.09.2026	137	182...202	100.0...111.0
6	Носовая смотровая площадка	53	202...215	111.0...118.0

Технические требования
1. Уровень палубы z = 8.60 м от основной плоскости. Кают на палубе – 0.
2. Размеры в миллиметрах, ось х – от кормового перпендикуляра, шпация практическая 550 мм.
3. Красные линии – водонепроницаемые переборки трюма, тонкие – границы зон.
4. Коридоры 1.30 м в свету, дортовой проход главной палубы 1.00 м, двери кают 0,70 (М4 – 0,90) м.
5. Коды кают – Э эконо, С стандарт, Б бизнес, Л люкс, Сем семейная, Эк экипаж, М4 – доступная.
УЖЦ ОСК 2026 · «Волжский Горизонт» · ПБ «Без границ»

Общее расположение. Солнечная палуба

Волжский Горизонт · L = 140.0 м · B = 16.5 м · T = 1.26 м · 208 пасс.	
ВГ-2026 ОР-03 солнечная палуба	Масштаб 1 : 200
Корпус сталь D36, надстройка АМз5	Формат А1

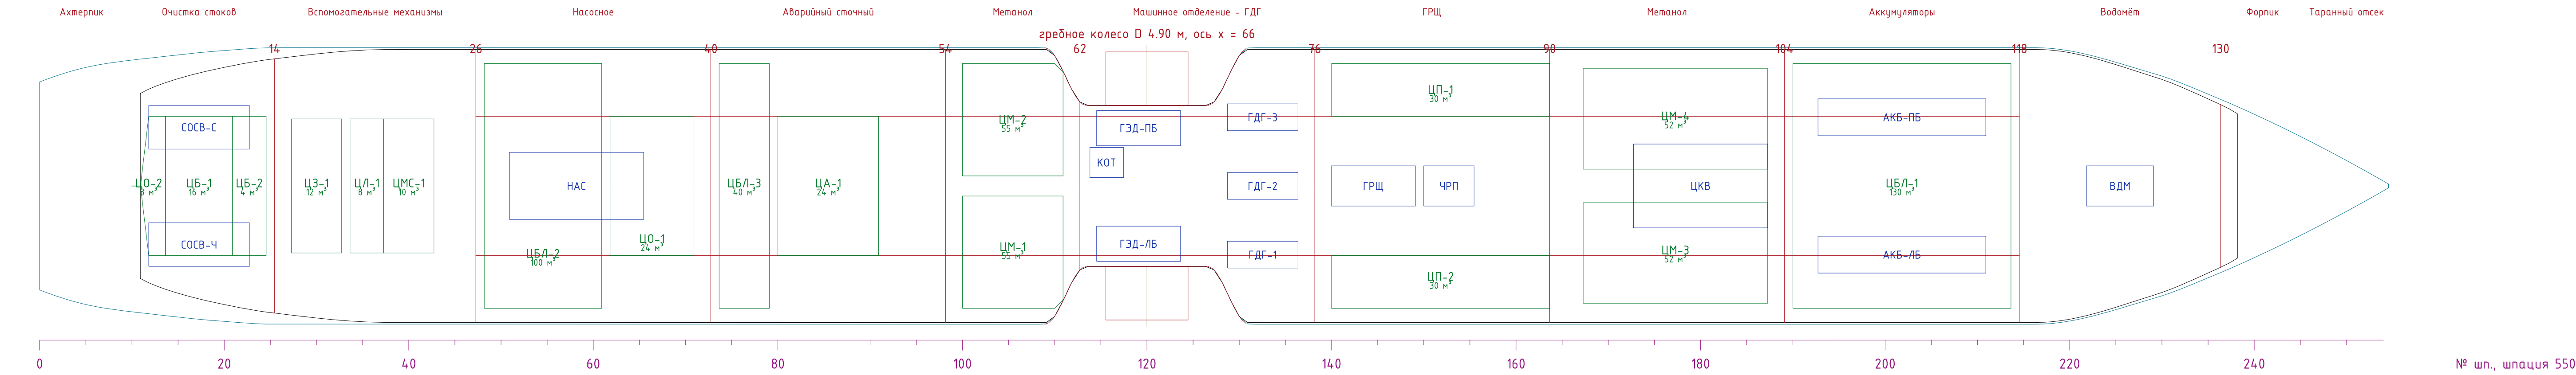

№	Код	Наименование	х, м	у, м	z, м	V, м³	Масса, т
1	ЦМ-1	Метанол, кормовая группа ЛБ	55.0..61.0	-7.3...-0.6	0.10..0.90	55	43.5
2	ЦМ-2	Метанол, кормовая группа ПБ	55.0..61.0	0.6...7.3	0.10..0.90	55	43.5
3	ЦМ-3	Метанол, носовая группа ЛБ	92.0..103.0	-7.0...-1.0	0.10..0.90	52	41.1
4	ЦМ-4	Метанол, носовая группа ПБ	92.0..103.0	1.0...7.0	0.10..0.90	52	41.1
5	ЦЗ-1	Запальное топливо	15.0...18.0	-4.0...4.0	0.10..0.90	12	10.3
6	ЦП-1	Пресная вода ЛБ	77.0...90.0	4.2...7.3	0.10..0.90	30	30.0
7	ЦП-2	Пресная вода ЛБ	77.0...90.0	-7.3...-4.2	0.10..0.90	30	30.0
8	ЦО-1	Очищенные серые воды	34.0..39.0	-4.2...4.2	0.10..0.90	24	24.0
9	ЦО-2	Очищенные чёрные воды	5.5...7.5	-4.2...4.2	0.10..0.90	8	8.0
10	ЦБ-1	Буфер серых вод	7.5...11.5	-4.2...4.2	0.10..0.90	16	16.0
11	ЦБ-2	Буфер чёрных вод	11.5...13.5	-4.2...4.2	0.10..0.90	4	4.0
12	ЦА-1	Аварийный сточный	44.0..50.0	-4.2...4.2	0.10..0.90	24	24.0
13	ЦЛ-1	Льельные воды	18.5..20.5	-4.0...4.0	0.10..0.90	8	8.0
14	ЦМС-1	Масло и шлам	20.5...23.5	-4.0...4.0	0.10..0.90	10	9.0
15	ЦБЛ-1	Балласт носовой	104.5..117.5	-7.3...7.3	0.00..0.90	130	130.0
16	ЦБЛ-2	Балласт кормовой	26.5...33.5	-7.3...7.3	0.00..0.90	100	100.0
17	ЦБЛ-3	Балласт средний (дифферентовка)	40.5...43.5	-7.3...7.3	0.00..0.90	40	40.0
18	ГДГ-1	Главный дизель-генератор 600 кВт, двухтопливный	70.8...75.0	-4.9...-3.3	0.90..2.70	-	11.0
19	ГДГ-2	Главный дизель-генератор 600 кВт, двухтопливный	70.8...75.0	-0.8...0.8	0.90..2.70	-	11.0
20	ГДГ-3	Главный дизель-генератор 600 кВт, двухтопливный	70.8...75.0	3.3...4.9	0.90..2.70	-	11.0
21	ГЭД-ПБ	Гребной электродвигатель колеса 550 кВт с редуктором	63.0...68.0	2.4...4.5	0.90..2.70	-	14.0
22	ГЭД-ЛБ	Гребной электродвигатель колеса 550 кВт с редуктором	63.0...68.0	-4.5...-2.4	0.90..2.70	-	14.0
23	ГРЩ	Главный распределительный щит 690 В	77.0...82.0	-1.2...1.2	0.90..2.70	-	8.0
24	ЧРП	Преобразователи частоты ГЭД и водомёта	82.5...85.5	-1.2...1.2	0.90..2.70	-	4.0
25	АКБ-ПБ	Аккумуляторная батарея 300 кВт·ч	106.0..116.0	3.0...5.2	0.90..2.50	-	6.0
26	АКБ-ЛБ	Аккумуляторная батарея 300 кВт·ч	106.0..116.0	-5.2...-3.0	0.90..2.50	-	6.0
27	НАС	Насосное отделение - балластные, пожарные, санитарные насосы	28.0...36.0	-2.0...2.0	0.90..2.30	-	9.0
28	СОСВ-Ч	Станция очистки чёрных стоков	6.5...12.5	-4.8...-2.2	0.90..2.50	-	6.0
29	СОСВ-С	Станция очистки серых стоков	6.5...12.5	2.2...4.8	0.90..2.50	-	5.0
30	КОТ	Котёл утилизационный с подогревом	62.6...64.6	0.5...2.3	0.90..2.60	-	6.5
31	ЦКВ	Центральный кондиционер и чиллеры	95.0...103.0	-2.5...2.5	0.90..2.60	-	12.0
32	ВДМ	Носовой водомёт 250 кВт с приводом	122.0..126.0	-1.2...1.2	0.30...180	-	4.5


Технические требования

- Второе дно z = 0...0.90 м. Цистерны второго дна между продольными переборками у = ±4.15 м и обшивкой.
- Метанол - в цистернах с коффердамами по торцам (1,0 м) и бортам, вентиляция и газоотвод в дымовую трубу.
- Всего 17 цистерн, 650 м³, масса содержимого при полном запасе 602 т (балласт пустой).
- Машинное отделение 62...76 м вокруг колёс - три ГДГ по 600 кВт, два ГЭД колёс по 550 кВт с редукторами.
- Красные линии - водонепроницаемые переборки (12 шт.), высота до главной палубы 3.0 м.

УЖЦ ОСК 2026 · «Волжский Горизонт» · ПБ «Без границ»

Трюм и второе дно. План цистерн и механизмов

Волжский Горизонт · 17 цистерн · 650 м³ · метанол 215 м³	
ВГ-2026 ОР-04 трюм и второе дно	Масштаб 1 : 200
Корпус сталь D36	Формат А1

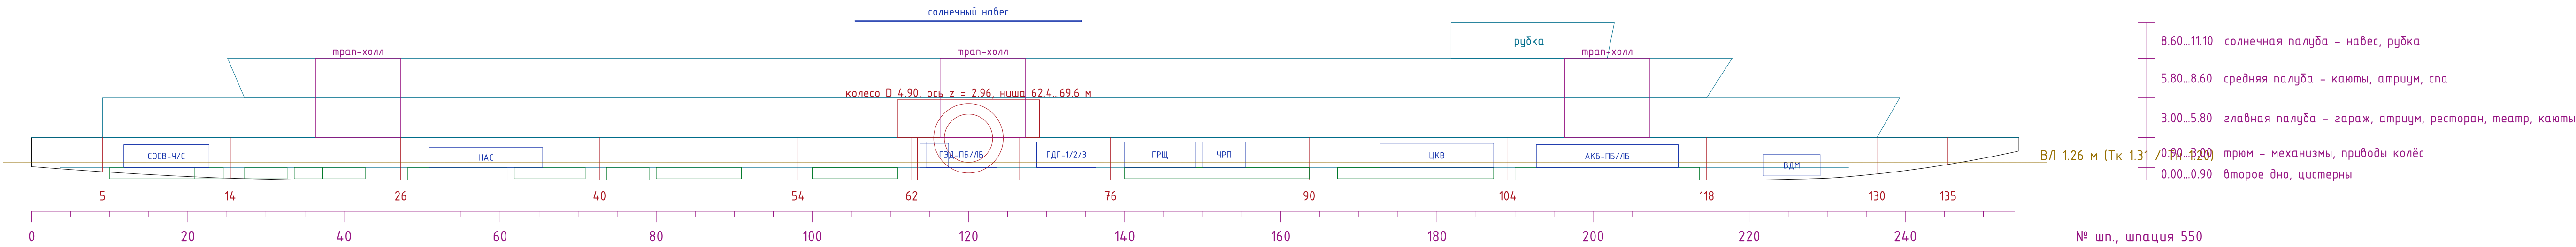

Палуба	х, м	Помещения
главная	0..5	Кормовая терраса, транцевая аппарель
главная	5..20	Гараж на 4 автомобиля класса Б, комплекс высадки на берег
главная	20..26	Кормовой трап-холл, лифт, санузлы
главная	26..34	Блок экипажа - столовая, кают-компания, офисы, каюты экипажа по бортам
главная	34..58	Каюты стандарт по бортам, каюты экипажа внутри
главная	58..74	Атриум - ресепшен, лобби, главный трап, два лифта, галереи к колёсам
главная	74..84	Камбуз, хлебопекарня, посудомоечная, раздаточная
главная	84..100	Главный ресторан
главная	100..108	Каюты стандарт по бортам, семейные внутри
главная	108..114	Носовой трап-холл, лифт
главная	114..124	Театр-лаунж - кино, концерты, лекторий, вечером клуб
главная	124..130	Носовой панорамный салон-обсерватория
главная	130..140	Открытая носовая палуба, якорно-швартовное устройство
средняя	15..20	Детский и подростковый клуб, творческая мастерская
средняя	20..26	Кормовой трап-холл, лифт
средняя	26..58	Каюты стандарт по бортам, семейные и эконом внутри
средняя	58..74	Верхний ярус атриума - галереи, бар-лаунж, фитнес ПБ
средняя	74..108	Каюты люкс и бизнес по бортам, семейные и эконом внутри
средняя	108..114	Носовой трап-холл, лифт
средняя	114..118	Спа - сауна, хаммам, процедурные
солнечная	15..26	Кормовая зона - шезлонги, бункероочный пост метанола ПБ
солнечная	26..58	Солярий, складные тенты
солнечная	58..74	Солнечные модули 24 кВт над атриумом, световой фонарь
солнечная	74..100	Прозрачная зона, спортплощадка, низкая дымовая труба
солнечная	100..111	Рулевая рубка
солнечная	111..118	Носовая смотровая площадка


Технические требования

- Продольный разрез по ДП. Высоты от основной плоскости, м.
- Габаритная высота от ВЛ 9,90 м, рубка стационарная, самый низкий мост маршрута 13,3 м.
- Красные линии - водонепроницаемые переборки трюма (12 шт.).
- Колёса на миделе в бортовых нишах, ось х = 66 м. Кожух в объёме первого яруса, над ним атриум.

УЖЦ ОСК 2026 · «Волжский Горизонт» · ПБ «Без границ»

Продольный разрез. Обозначение ярусов


Волжский Горизонт · L = 140,0 м · Н = 3,0 м · Т = 1,26 м	
ВГ-2026 ОР-05 продольный разрез	Масштаб 1 : 250
Корпус сталь D36, надстройка АМз5	Формат А1

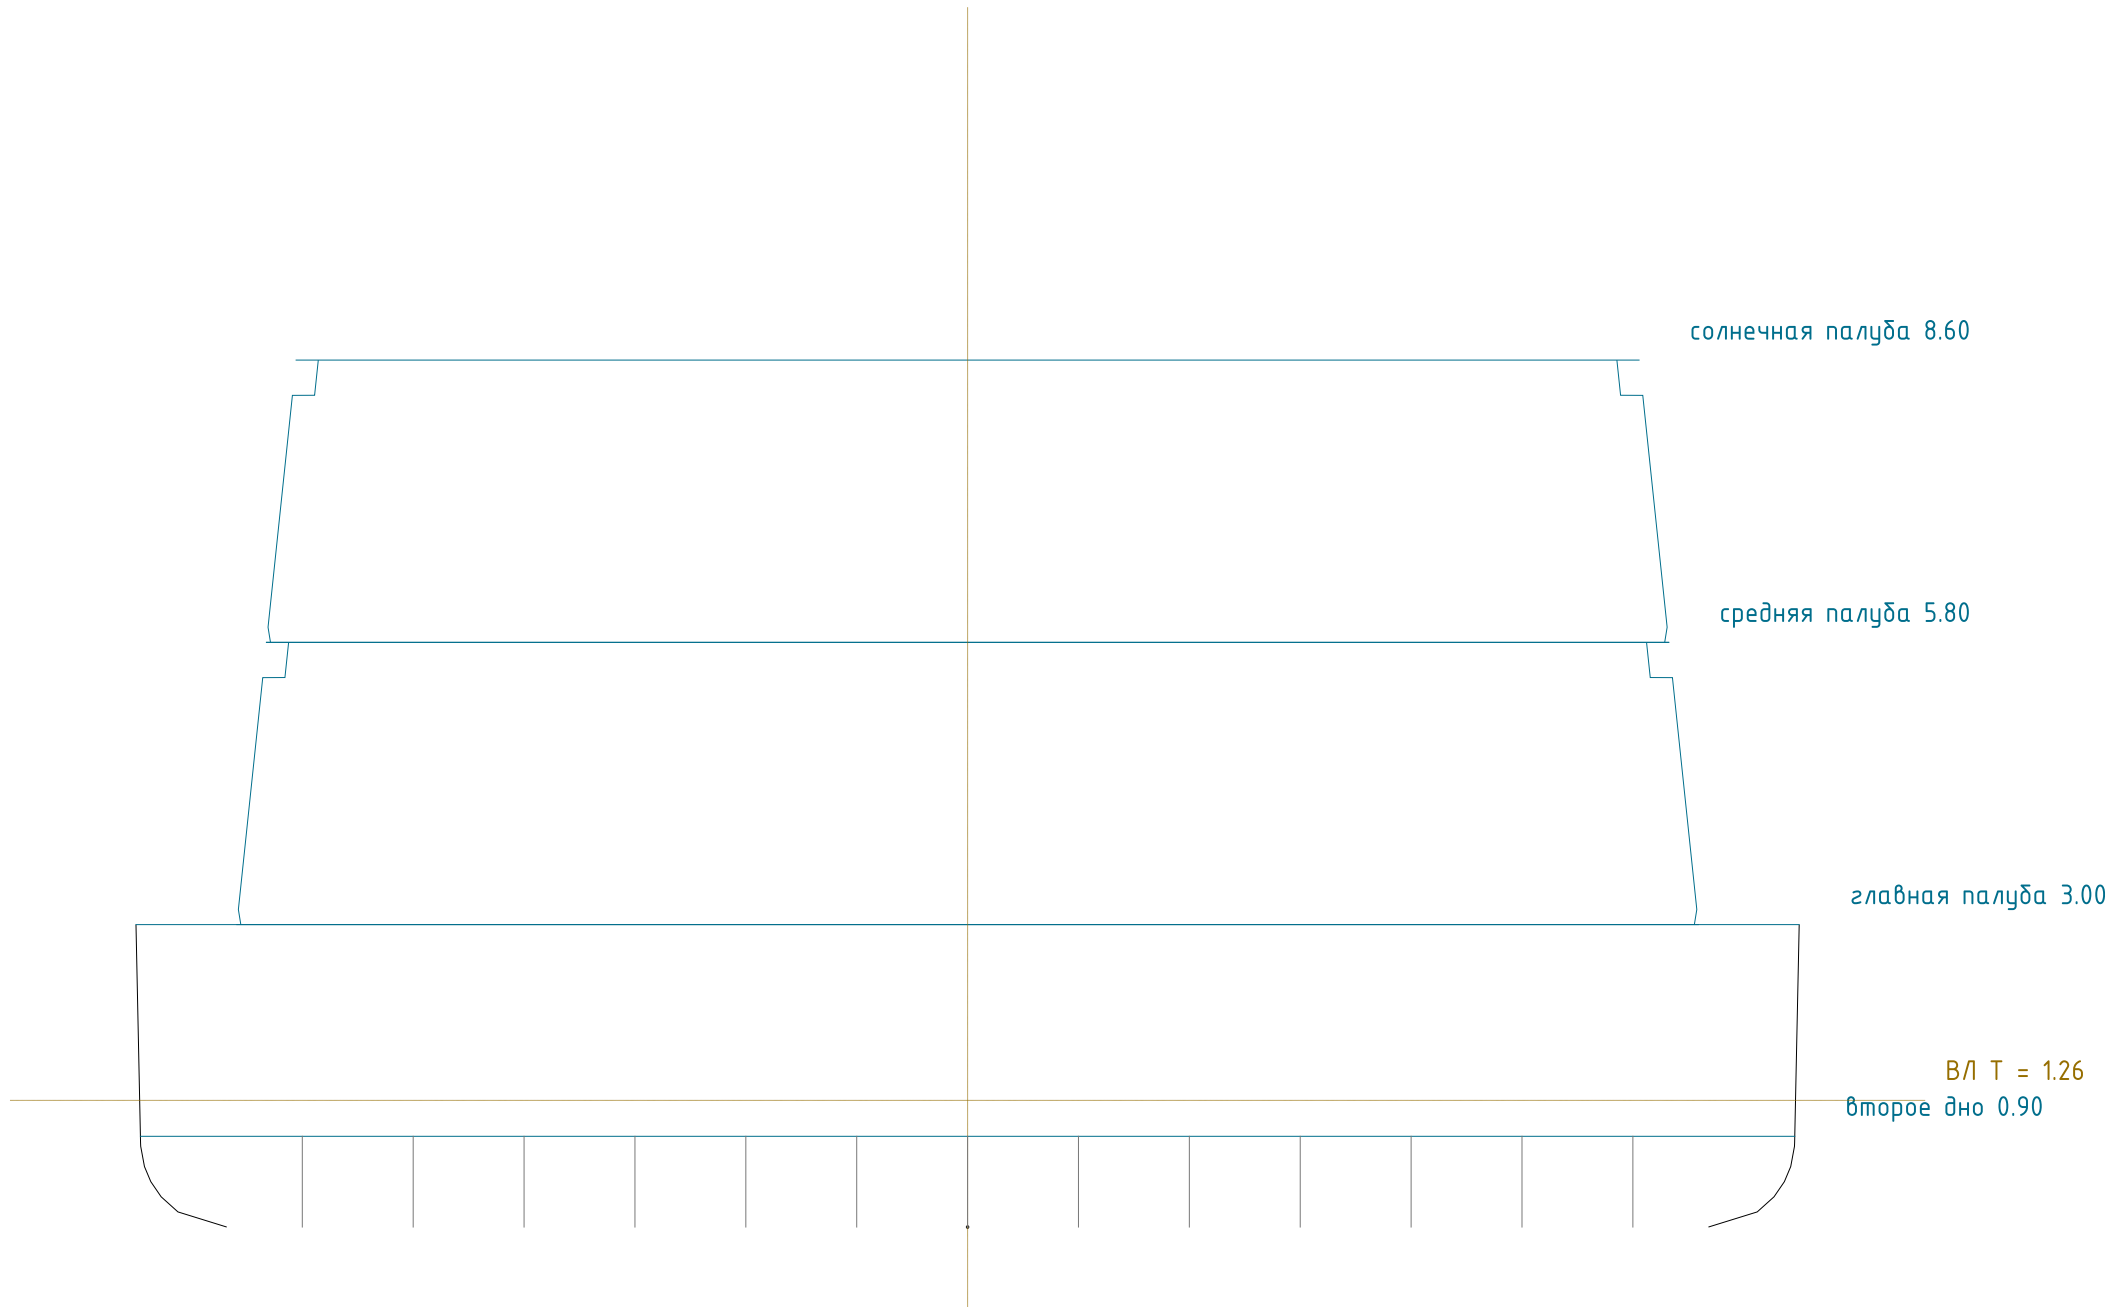

Сечение А-А, шп. 145 (х = 80 м), полная ширина

В = 16500 Н = 3000 Т = 1256

№	Лист обшивки и настила	t, мм	Профиль набора	h x t + b x t, мм
1	горизонтальный киль	11	вертикальный киль	1200 x 12
2	днище	8	днищевой стрингер	1200 x 10
3	скала	8	флор сплошной	1200 x 9
4	борт в районе ВЛ	8	флор в машинном	500 x 9
5	борт ниже пояса	7	ребро днища	140 x 8 + 60 x 10
6	ширстрек	10	ребро второго дна	120 x 8 + 50 x 8
7	второе дно	7	ребро палубы	120 x 8 + 50 x 8
8	настил главной палубы	8	шпангоут	120 x 8 + 50 x 8
9	палубный стрингер	12	рамный шпангоут	500 x 10 + 150 x 12
10	переборки водонепроницаемые	6	бортовой стрингер	400 x 9 + 100 x 10
11	настил средней палубы	6	карлингс	600 x 10 + 180 x 12
12	настил солнечной палубы	6	рамный димс	500 x 10 + 150 x 12
13	борта надстройки	5	холостой димс	120 x 8 + 50 x 8
14	рубка	5	стойка переборки	180 x 8 + 70 x 10

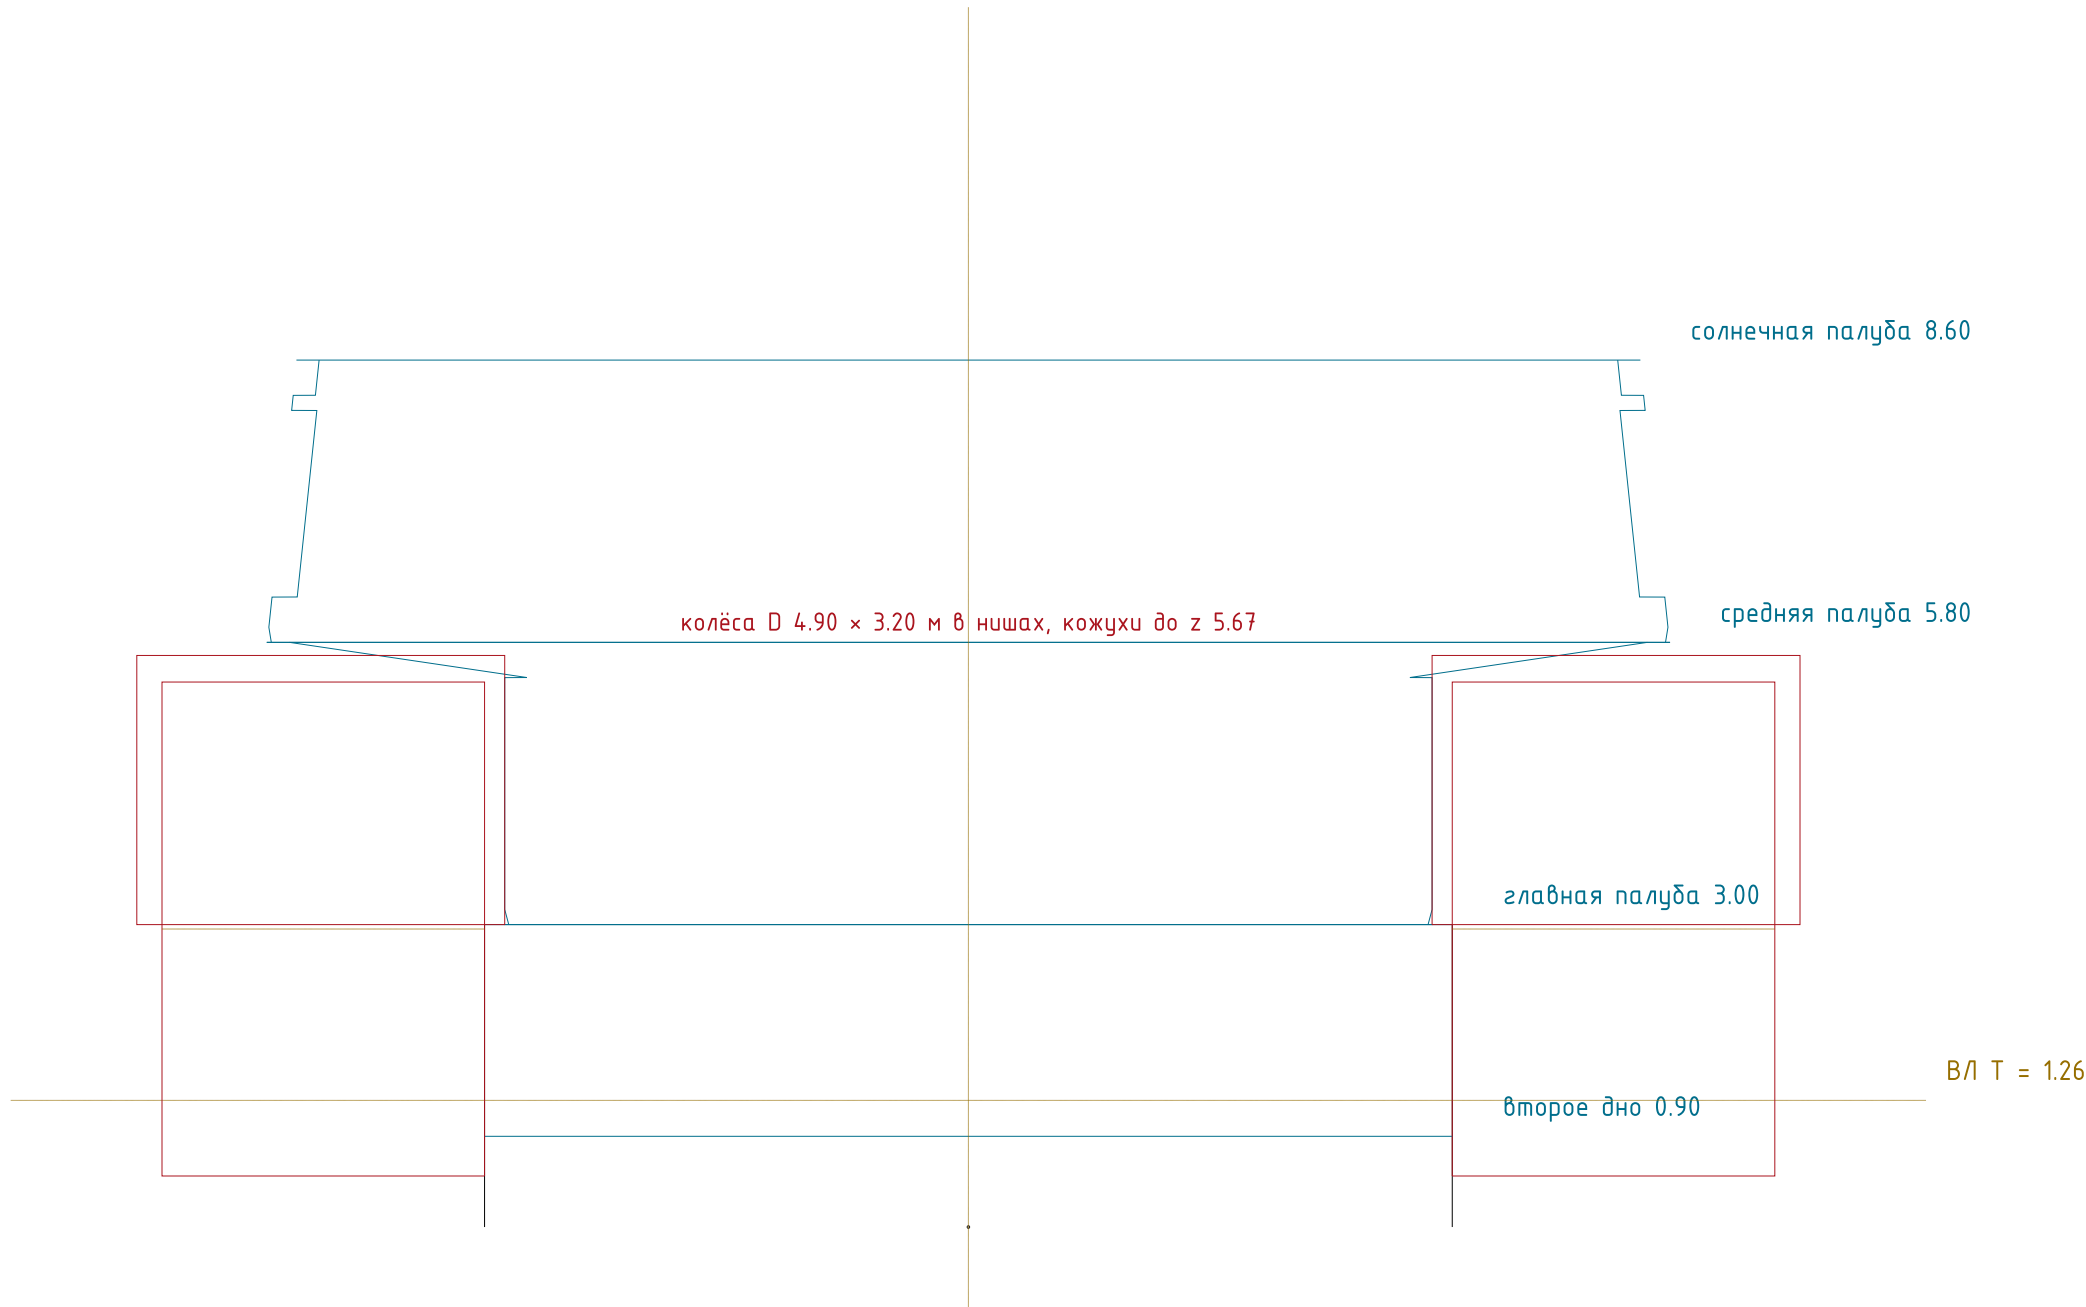

Сечение Б-Б, по оси колёс (х = 66 м)


Технические требования

- Смешанная система набора – продольная в днище, втором дне и главной палубе, поперечная по бортам.
- Шпация 550 мм, рамная 2200 мм. Корпус – сталь Д36 (ГОСТ Р 52927), надстройка – АМз5.
- Эквивалентный брус (сечение А-А) – А = 6342 см², z0 = 136 м, I = 1.023 мД, W палубы 0.622 м³, W днища 0.754 м³.
- В сечении Б-Б борт вырезан нишей колеса от киля до главной палубы, момент передают переборки ниш и настилы.

УЖЦ ОСК 2026 · «Волжский Горизонт» · ПБ «Без границ»

Поперечные сечения – по шп. 145 и по оси колёс







Волжский Горизонт · В = 16,5 м · Н = 3,0 м · Т = 1,26 м	
ВГ–2026 ОР–06 поперечные сечения	Масштаб 1 : 75
Сталь Д36 ГОСТ Р 52927	Формат А1

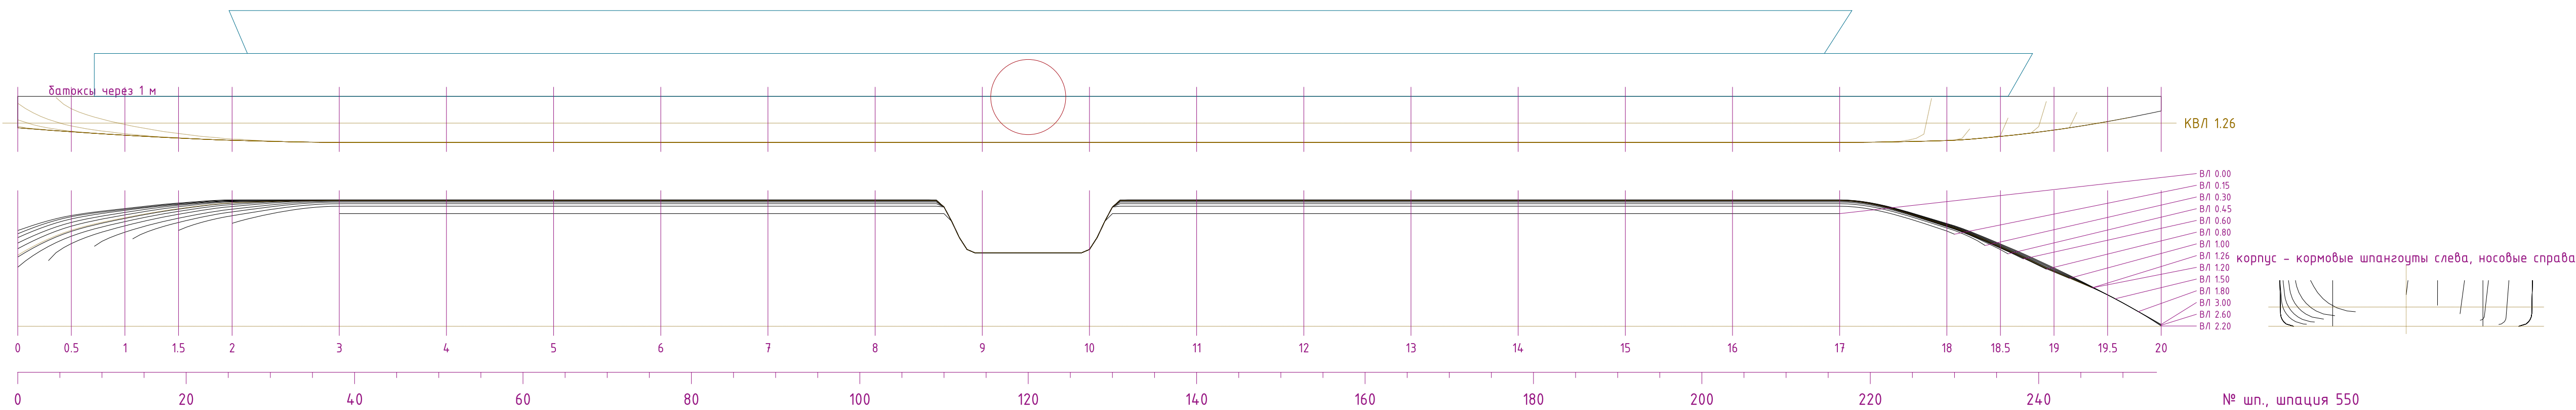

- Технические требования
1. Теоретический чертёж – бок (поднят на 12 м), полуширота, корпус. Ординаты – по плазовой таблице с нишами колёс.
 2. L = 140.0, B = 16.5, H = 3.00, T = 1.26 м, δ = 0.850, α = 0.919, β = 0.982, V = 2378 м³.
 3. 20 теоретических шпангоутов через L/20 = 7.00 м и полушпангоуты в оконечностях, ватерлинии по плазовой таблице.
 4. Обвод – плоское днище, скуловая дуга, прямой борт с развалом. Ниши колёс 62.4...69.6 м от киля до палубы.

УЖЦ ОСК 2026 · «Волжский Горизонт» · ПБ «Без границ»

Теоретический чертёж	
Волжский Горизонт · L = 140.0 · B = 16.5 · H = 3.0 · T = 1.26	
ВГ-2026 ОР-07 теоретический чертёж	Масштаб 1 : 250
-	Формат А1

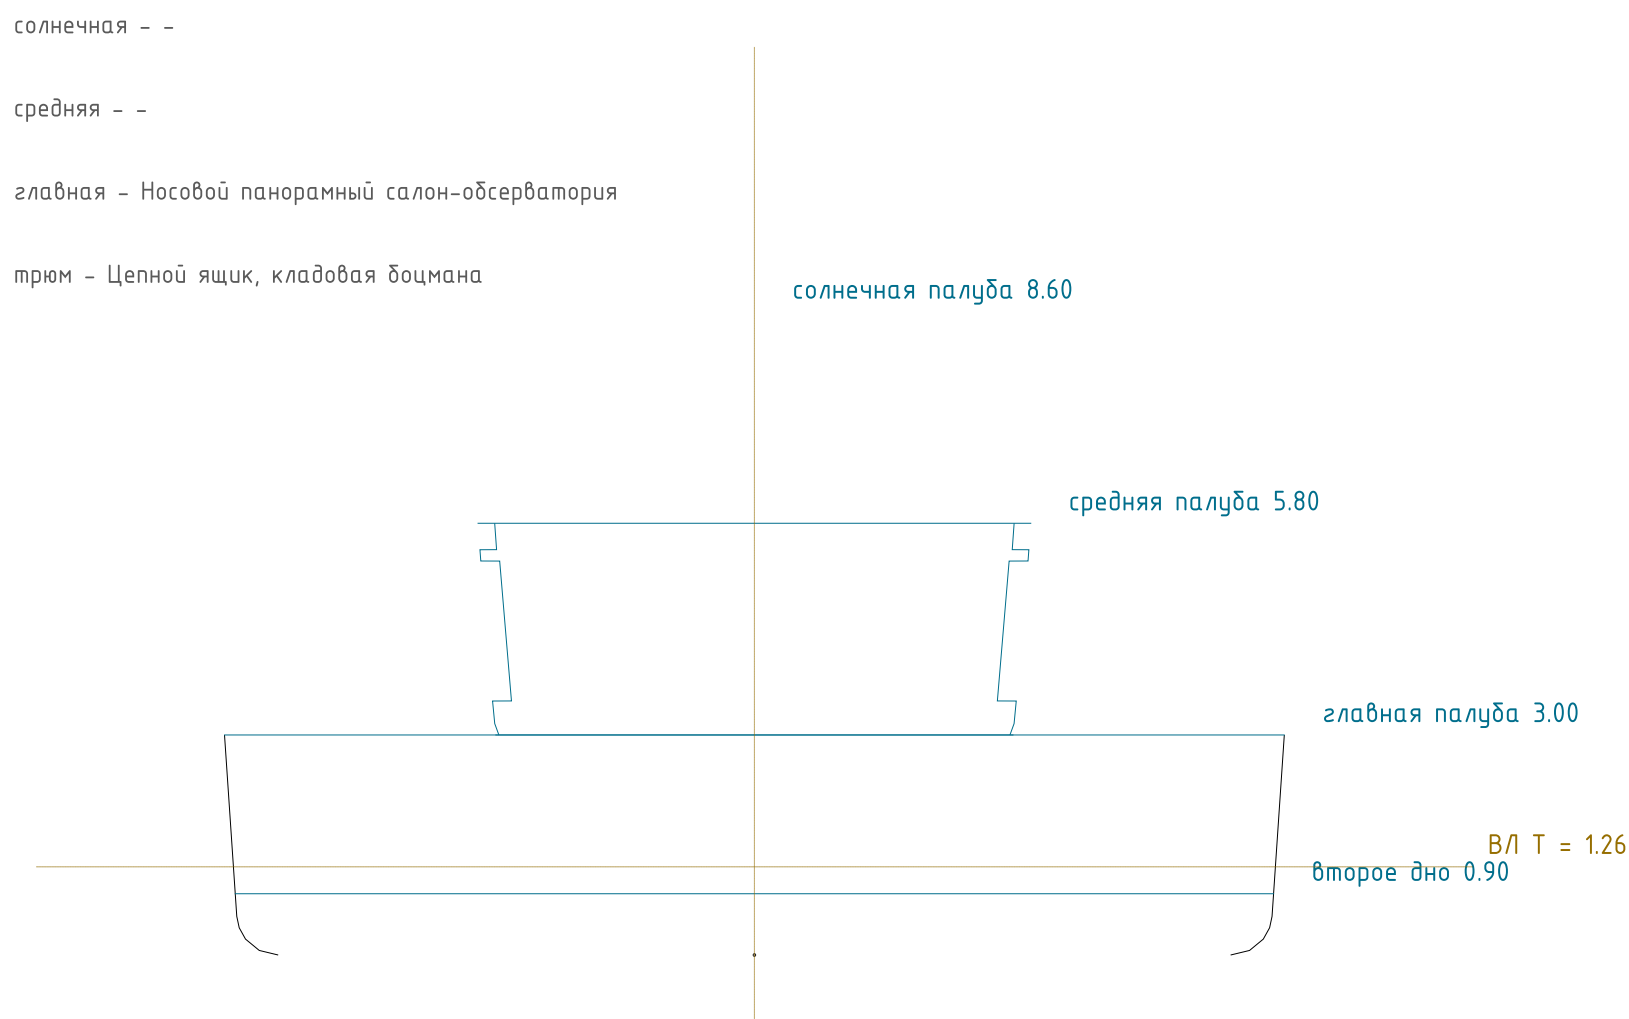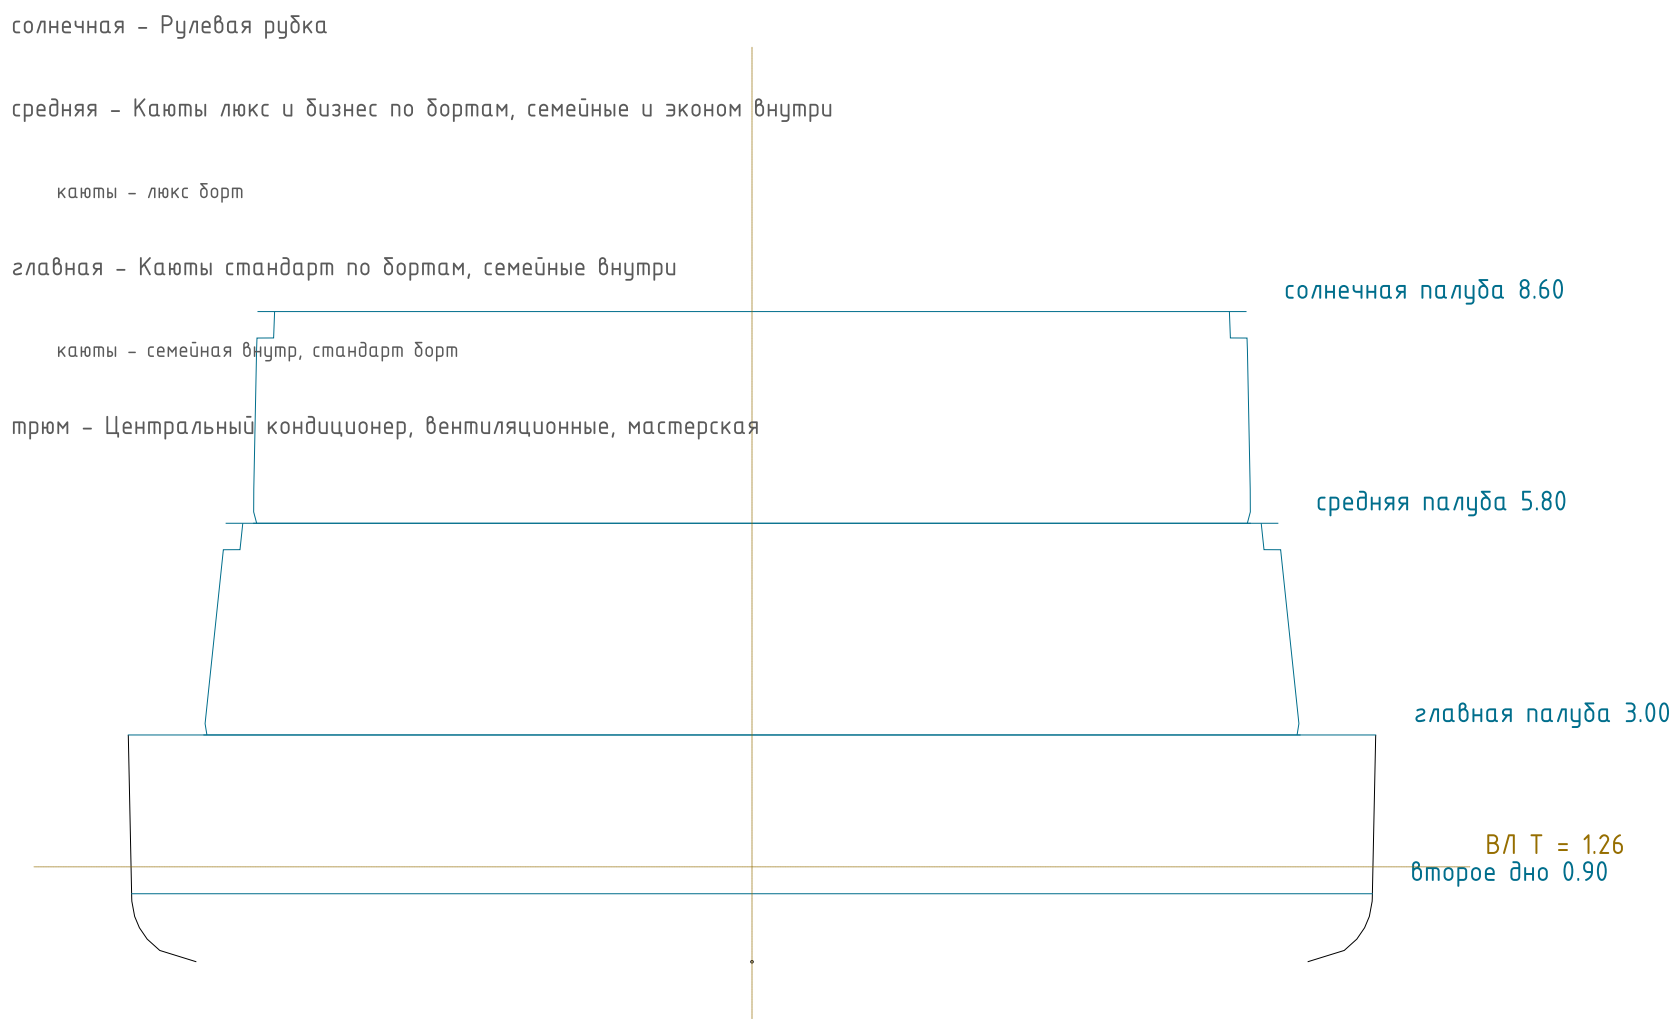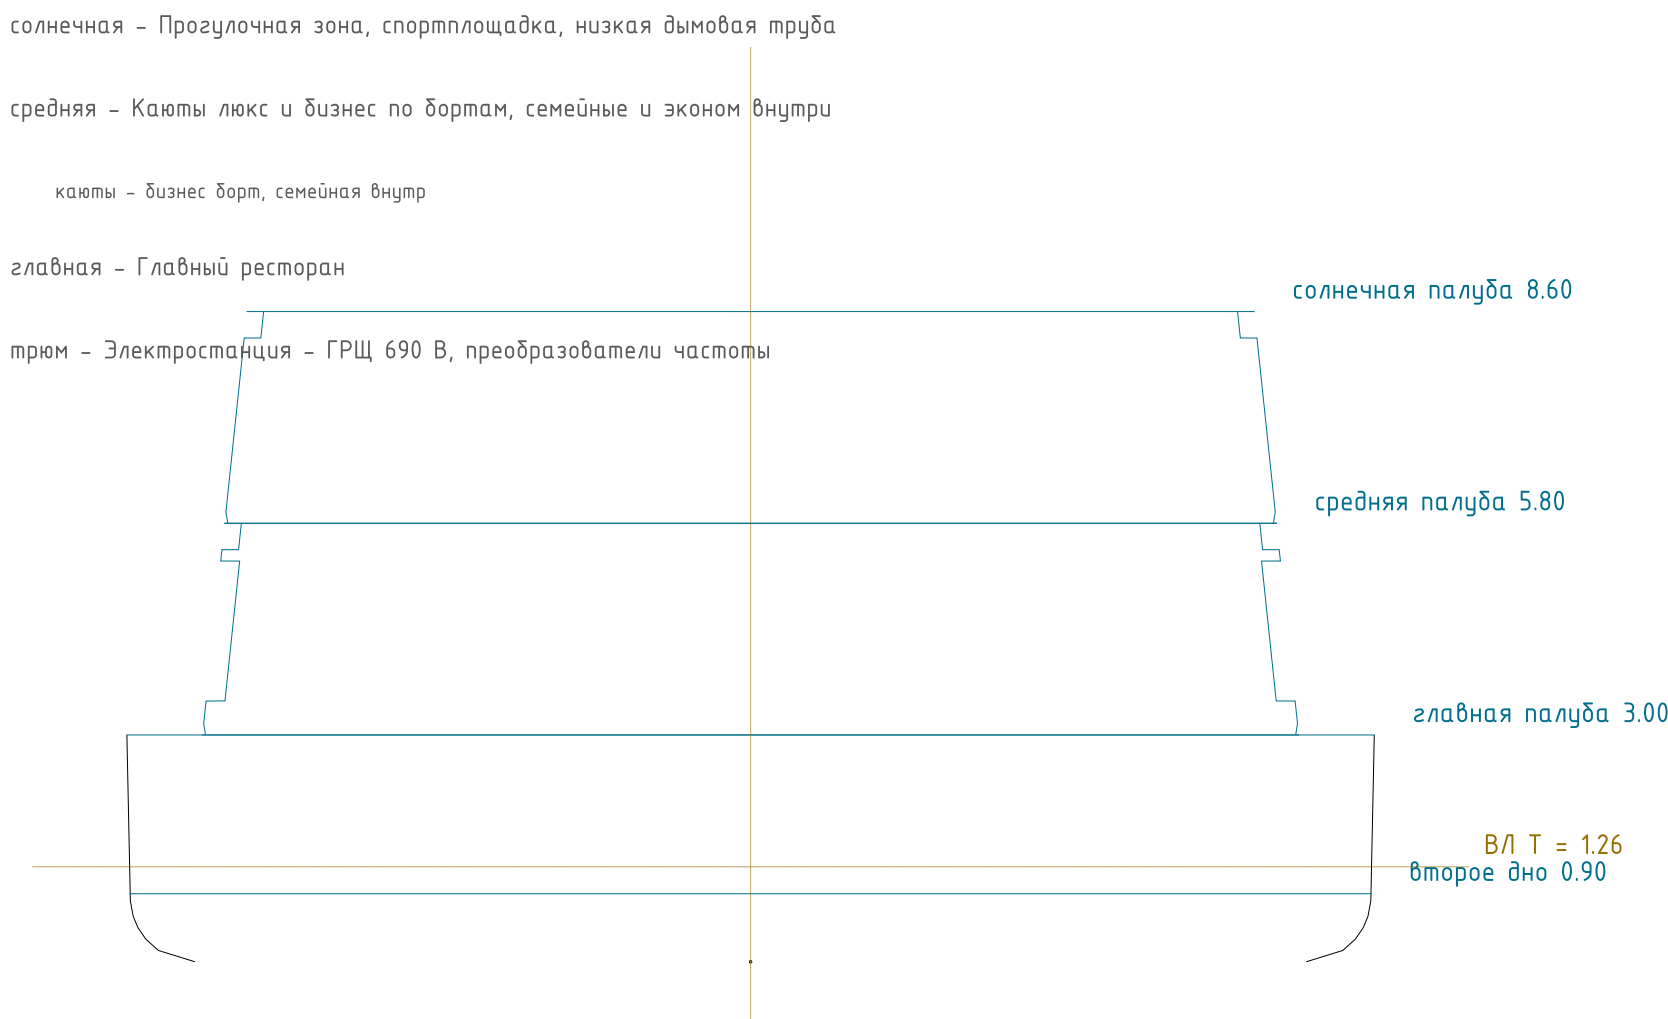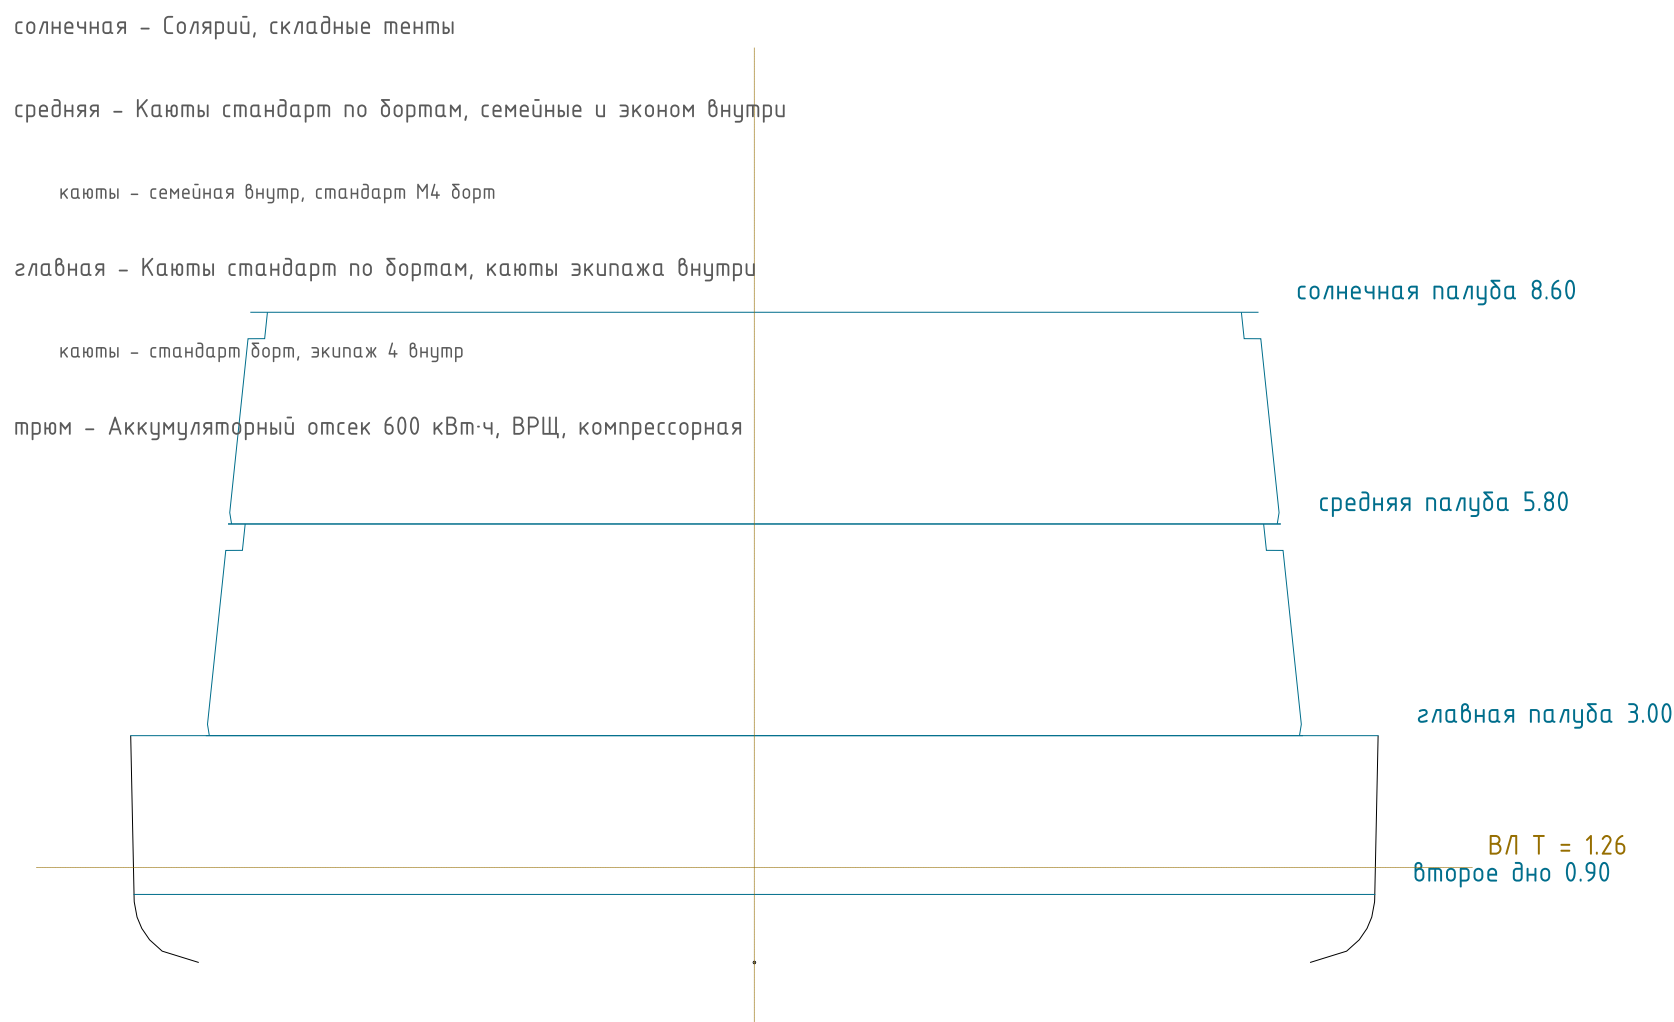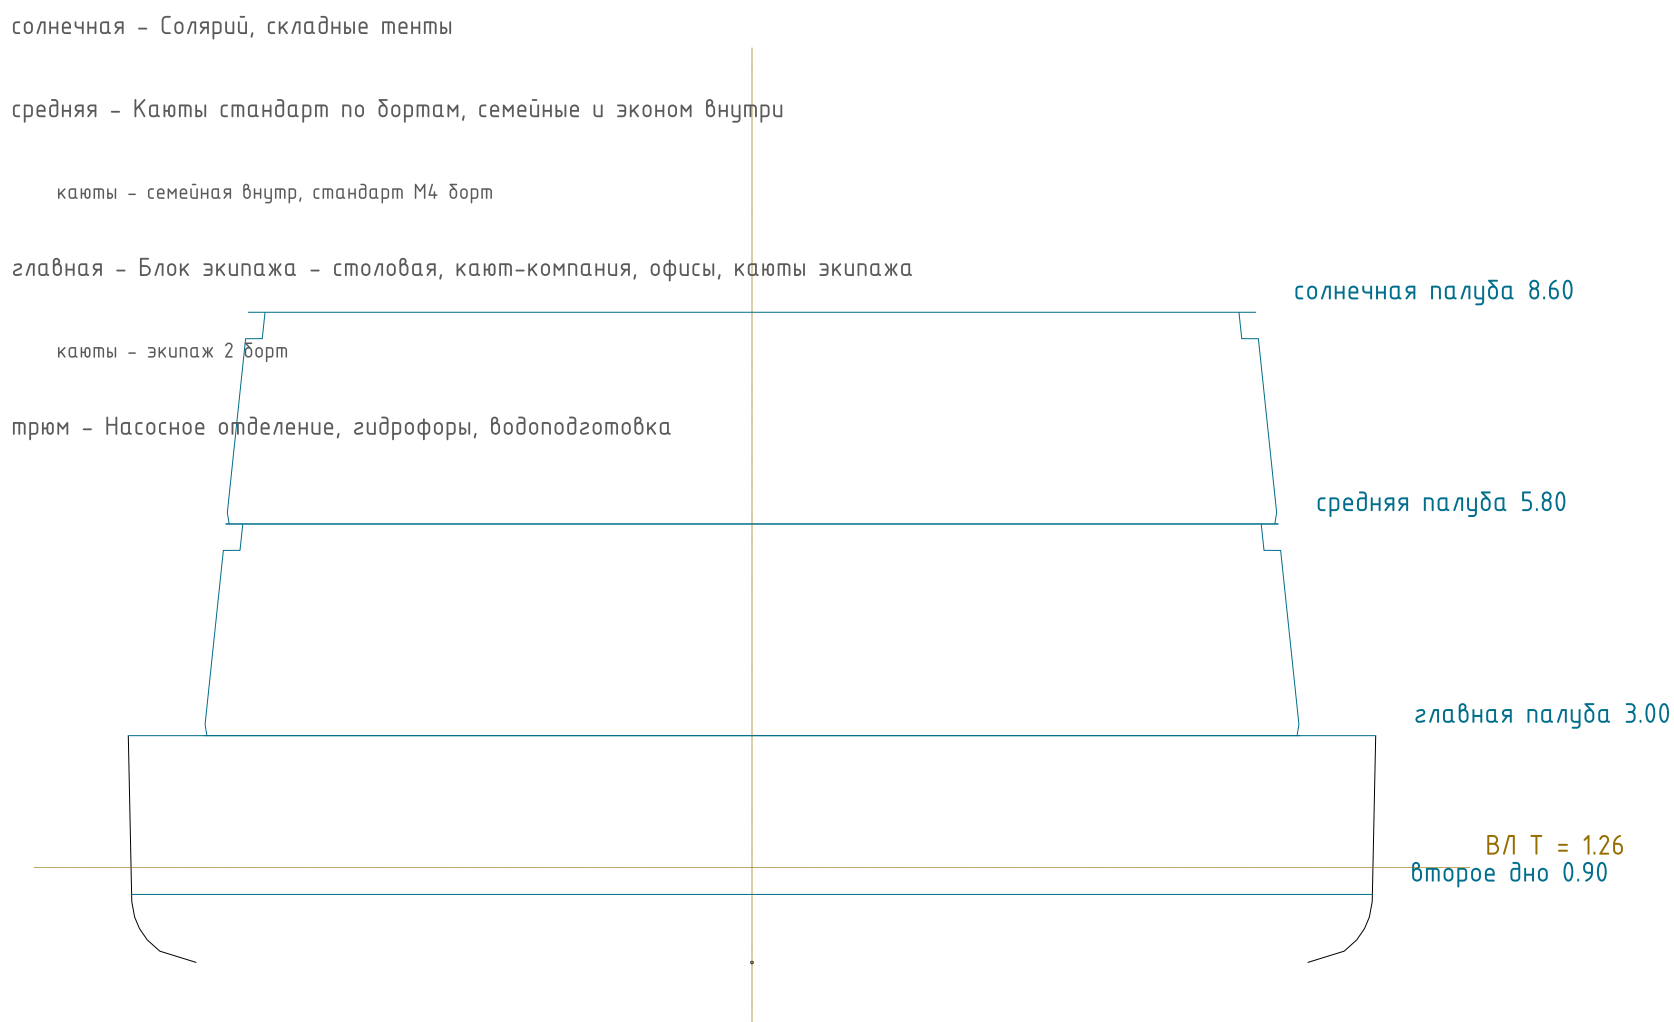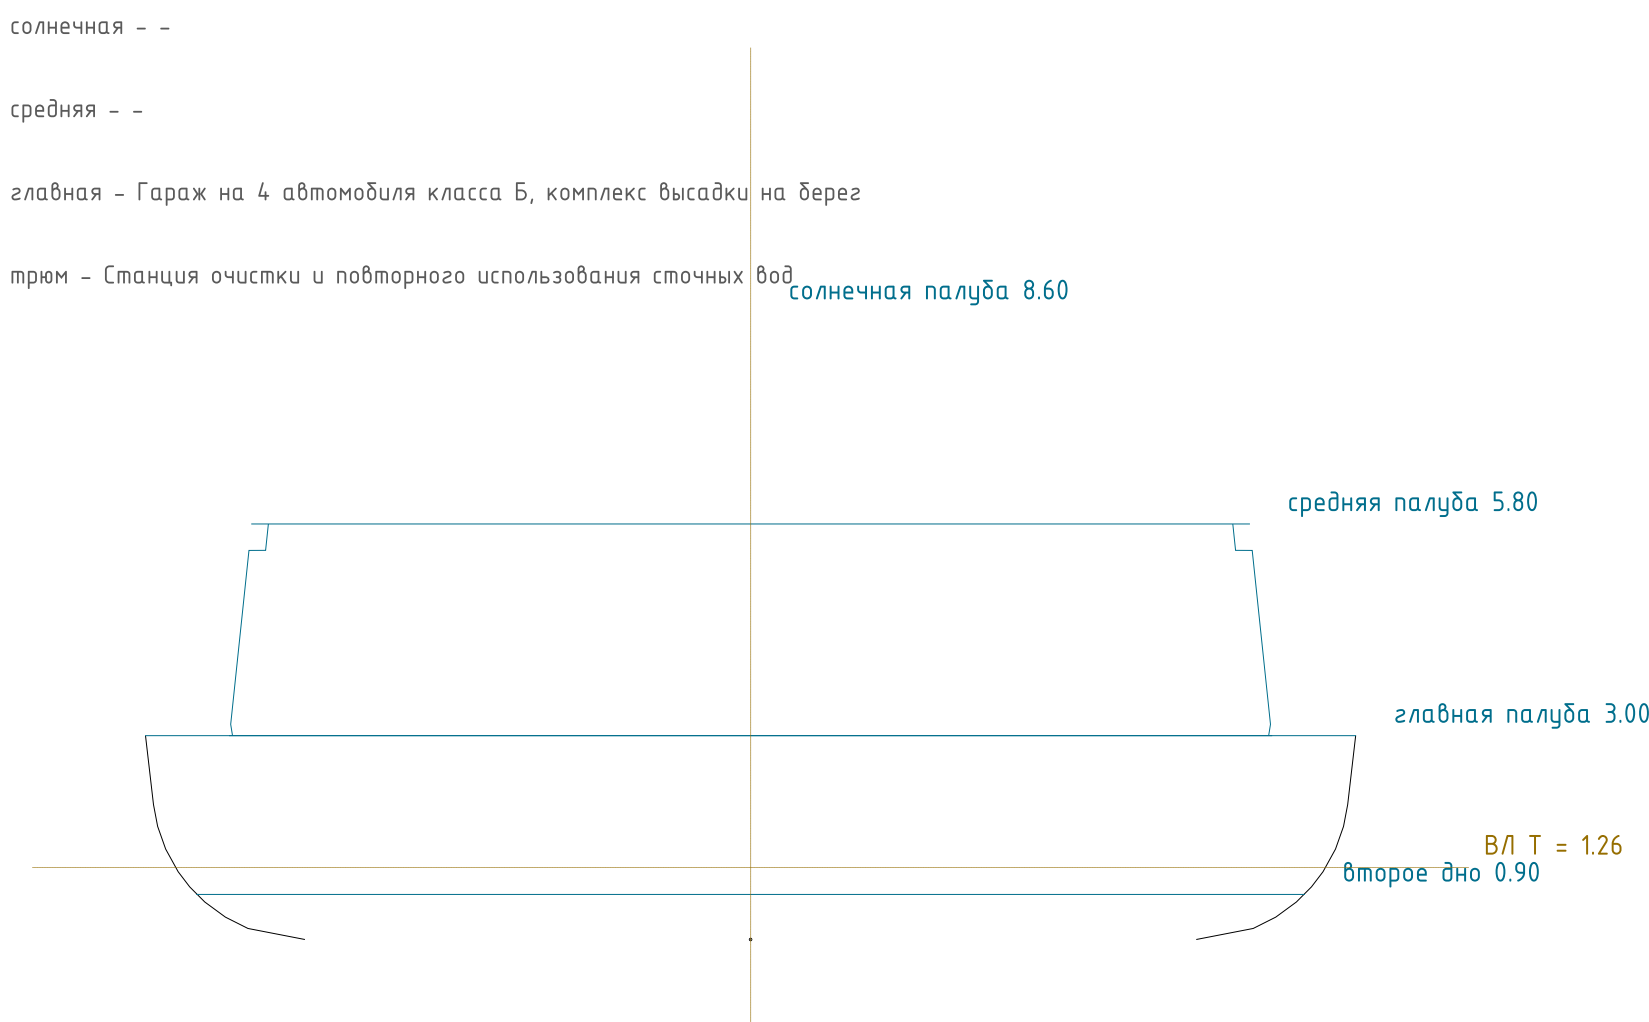

Технические требования 1. Сечения по длине корпуса - положение по шпангоутам и по x от кормового перпендикуляра. 2. На каждом сечении. Обвод корпуса (в районе колёс - с нишей), ярусы надстройки, уровни палуб, ватерлиния Т = 1.26 м. 3. Состав помещений по уровням - по общему расположению ОР-01..04, каюты - по расстановке рядов. 4. Сечения по нишело и по оси колёс с набором и таблицей связей - лист ОР-06. УЖЦ ОСК 2026 · «Волжский Горизонт» · ПБ «Без границ»	
Поперечные сечения по длине судна - x = 10, x = 30, x = 50, x = 85, x = 105, x = 125	
Волжский Горизонт · L = 140.0 м · В = 16.5 м · Т = 1.26 м	
ВГ-2026 ОР-08 сечения по длине	Масштаб 1 : 100
Сталь Д36 ГОСТ Р 52927	Формат А1